ISH-Template



קובץ טמפלט מקצועי לעבודה ב- REVIT

אלי שוקרי | אדריכל

simple to know

החתום מטה אינו עובד בחברת Autodesk ואינו פועל מטעמה

נעים מאוד,
אלי שוקרי,

אדריכל,
מדריך ומטמיע Revit,
כותב הבלוג "איש הרויט",
מנהל בית הספר המקוון ללימודי Revit.
בוגר אוניברסיטת אריאל.

הטמפלט שלפניכם נוצר אחרי שנים של עבודה ברוויט
כאדריכל ואחרי שהוטמע במעל 100 משרדים בארץ

בדפים הבאים תוכלו להתרשם ממה מורכב הטמפלט ואיך הוא יוכל
לקצר לכם זמנים ובעיקר לעבוד במקצועיות נוחות וסדר מקסימלי

אני מזמין אתכם ליצור איתנו קשר לכל שאלה
ועניין לגבי הטמפלט וההכשרות שלנו
במייל info@ish.co.il
טלפון/וואטסאפ 054-8811651

בהצלחה



REVIT הינה תוכנה של חברת Autodesk
החתום מטה אינו עובד ואינו פועל מטעם החברה
ספר זה אינו מטעם חברת Autodesk ולא הומלץ על ידיה

© כל הזכויות שמורות לאלי שוקרי 2018

איך אנחנו עוד יכולים לעזור לכם ?

- בלוג רוויט
- ספר רוויט
- קורס רוויט מקיף
- קורס רוויט למתקדמים
- קורס רוויט בניית משפחות
- תוכנית לווי ללימוד רוויט
- קבצי משפחות (נגרות, חשמל, דלת)

לכל הפרטים לחצו כאן

כל הזכויות שמורות לאלי שוקרי | איש אדריכלים בע"מ
www.ish.co.il | info@ish.co.il | 054-8811651


קובץ טמפלט מקצועי לאדריכלים ומעצבי פנים


קובץ טמפלט הוא כלי העבודה המרכזי שלכם


אבל הוא מורכב ממספר אלמנטים אותם תקבלו ברכישה


1. קורס מקוון המסביר איך לעבוד עם קובץ הטמפלט ולעשות בו התאמות
2. קובץ טמפלט עם המון הגדרות + קובץ קטלוג מאגד
3. 3 קטלוגים - קבצי רוויט בהם המון קבצי משפחות מוכנים לשימוש

הקבצים בנויים בגרסת 2016 ויעבדו בכל גרסה מ 2016 ומעלה

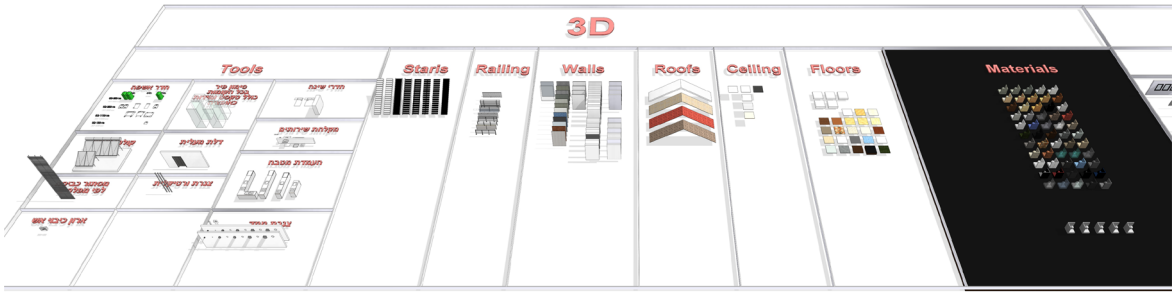

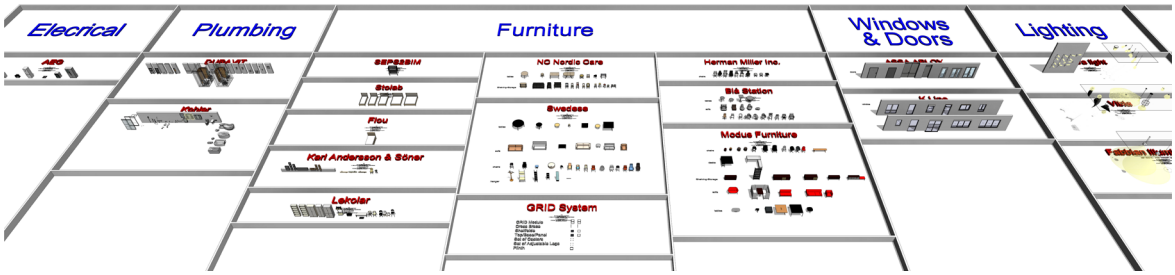

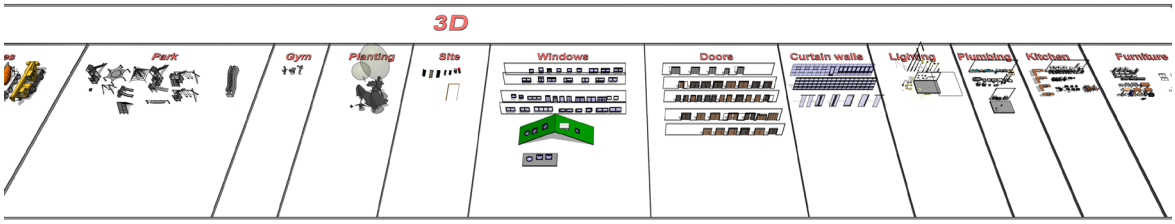

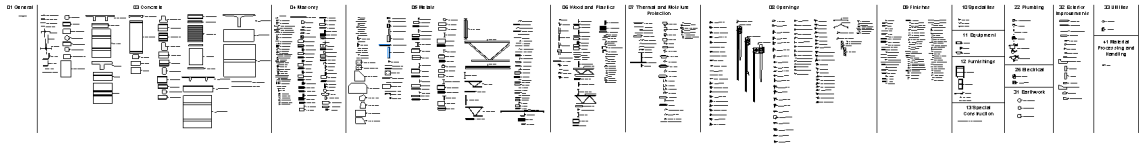

כל הזכויות שמורות לאלי שוקרי | איש אדריכלים בע"מ
www.ish.co.il | info@ish.co.il | 054-8811651
ISH simple to know


1

הטמעה

קורס מקוון להטמעת הטמפלט

גישה לקורס וידאו של מעל 3 שעות,
בסרטונים קצרים שיסביר לכם בדיוק

1. מה יש בטמפלט
2. איך לתפעל כל דבר ולעבוד נכון
3. איך להתאים את הטמפלט לצרכים שלכם

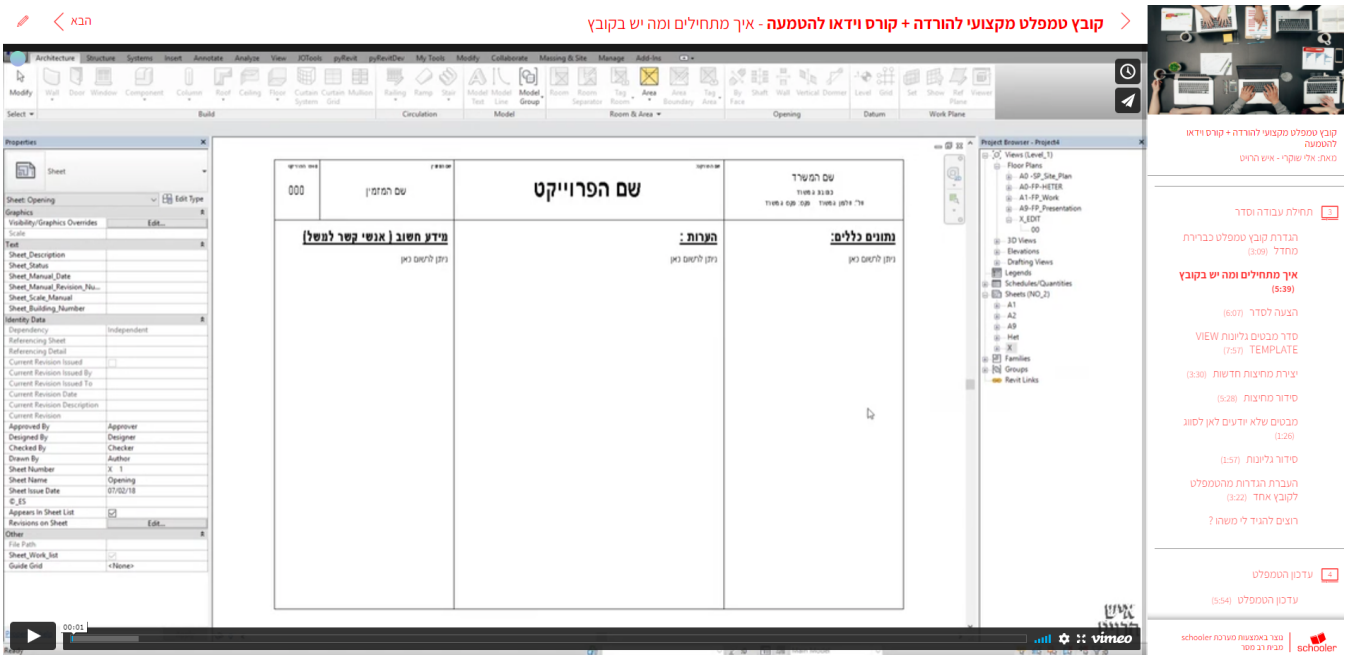

כל הזכויות שמורות לאלי שוקרי | איש אדריכלים בע"מ
www.ish.co.il | info@ish.co.il | 054-8811651
ISH simple to know

2

הטמפלט

קובץ הטמפלט

הקדמה

קובץ הטמפלט נבנה מתוך נסיון של שנים בעבודה על פרוייקטים שונים, והטמעת REVIT במשרדים רבים, מתוך ידע אישי ודרישות של משתמשים בנושא, ובעיקר מתוך רצון לקצר ולהפוך תהליכי עבודה לנוחים ויעילים כמה שיותר.

הקובץ מכיל הגדרות מכל הסוגים, בניית פרמטרים בהגדרה אישית, וחולש על רוב הכלים הקיימים בתוכנה.

ניהול הפרוייקט

בפתיחת הטמפלט, ובפתיחת כל פרוייקט שיפתח עם הטמפלט יופיע קודם כל מסך ניהול הפרוייקט, בו תוכלו לרשום לעצכמם ולעובדים שלכם סטטוסים, הערות, פרטי אנשים קשר וכל מידע שתרצו לטובת כל משתמשי הפרוייקט

שם המשרד כתובת המשרד טל': טלפון המשרד Mail : XXX@XXX.XX	שם הפרוייקט: **שם הפרוייקט**	שם המזמין שם המזמין	מספר הפרוייקט 000
נתונים כללים: ניתן לרשום כאן	**הערות :** ניתן לרשום כאן	**מידע חשוב (אנשי קשר למשל)** ניתן לרשום כאן	

כל הזכויות שמורות לאלי שוקרי | איש אדריכלים בע"מ
www.ish.co.il | info@ish.co.il | 054-8811651
ISH simple to know

View Template - תבניות תצוגה אוטומטיות


מעל 150 תבניות תצוגה לכל שימוש אפשרי

הנושא החשוב ביותר, הגדרות גרפיות מובנות אוטומטית למסמכים לכל שלבי הפרוייקט.


בהכנת כל מסמך בוחרים את ההגדרות המוכנות מראש והגרפיקה משתנה בהתאם.
פונקציה זו נועדה לשמור על גרפיקה אחידה במסמכים, ומאגדת בתוכנה המון הגדרות שאותם מיישמים ומשנים באופן גורף.

לדוגמה, גרפיקה של תוכנית להיתר, תכיל צביעת קירות לפי שימוש, קנ"מ, כיבוי רהיטים אבל לא כיבוי סניטריה, הצגת חתכי היתר בלבד, הצגת קו בנין וקו מגרש בצבעים שונים ועוד, והכל באופן אוטומטי.


הגדרות מוכנות מראש מחולקות לפי סוג מבטים תוכניות, חתכים, חזיתות, תלת מימד. לפי השלבים הבאים

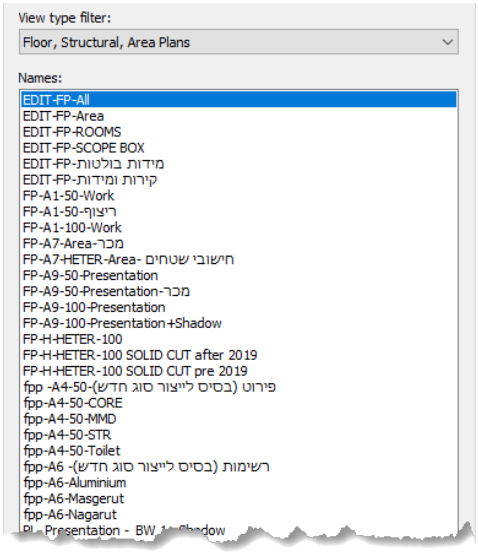


- תוכנית סביבה
- היתר
- תוכניות עבודה
- פירוטים (גרעין, ממד,שירותים, מדרגות)
- רשימות (אלומניום, מסגרות, נגרות)
- פריסות
- חישובי שטחים
- מכר
- מצגות
- תכנית ריצוף
- מבטי עריכה לעבודה נוחה
- תלת מימד, פרספקטיבי צבעוני / שחור לבן ועוד
- ועוד רבים נוספים

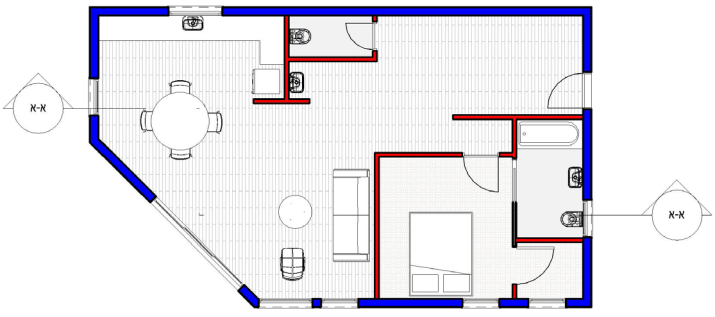


היתר

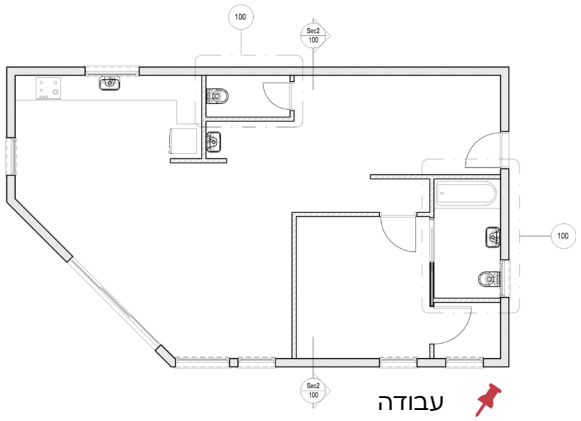

עבודה

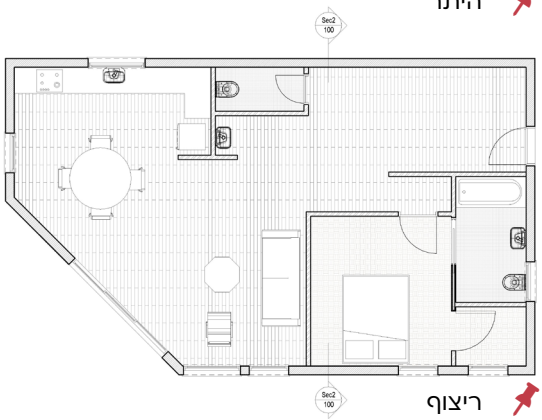

ריצוף

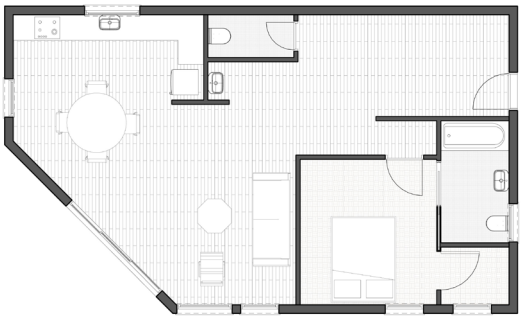

מכר


כל הזכויות שמורות לאלי שוקרי | איש אדריכלים בע"מ
www.ish.co.il | info@ish.co.il | 054-8811651
ISH simple to know







View Template - פרזנטציה 3D

בלחיצת כפתור לקבל את הגרפיקה המתאימה לכם
















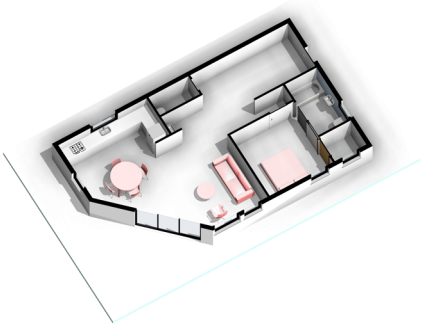


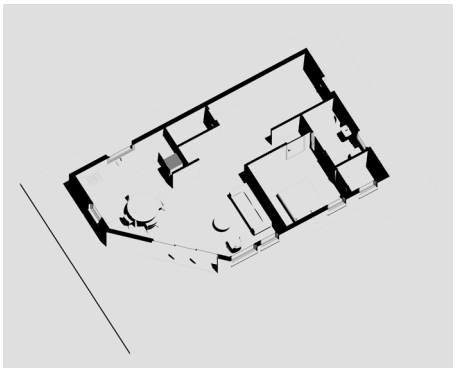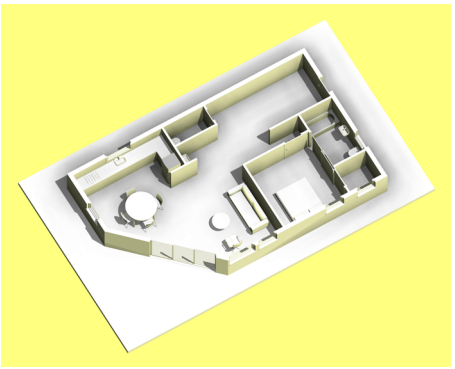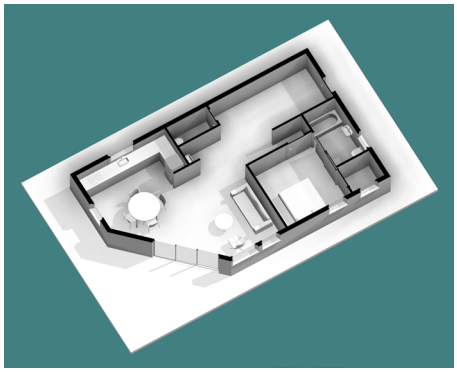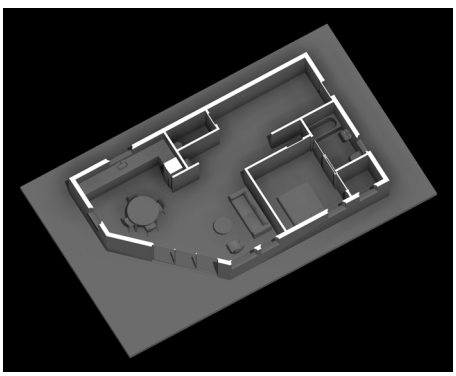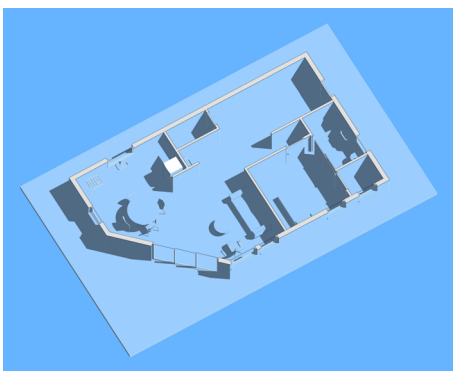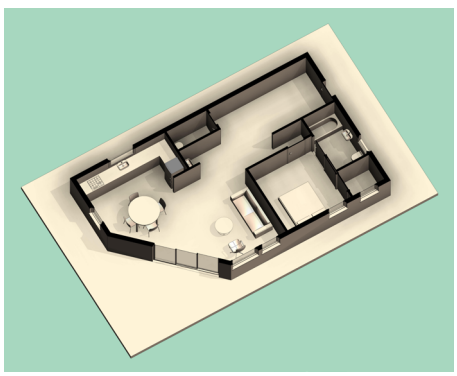כל הזכויות שמורות לאלי שוקרי | איש אדריכלים בע"מ
www.ish.co.il | info@ish.co.il | 054-8811651
ISH simple to know


View Template - פרזנטציה תוכניות

להציג ללקוח בשפה שהוא יבין

כל הזכויות שמורות לאלי שוקרי | איש אדריכלים בע"מ
www.ish.co.il | info@ish.co.il | 054-8811651
ISH simple to know

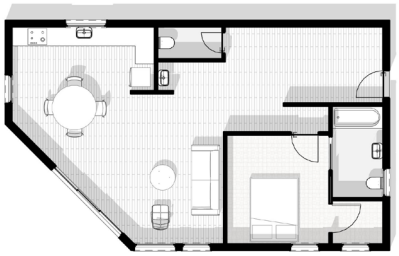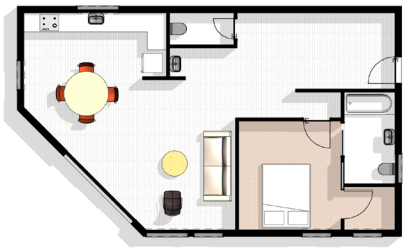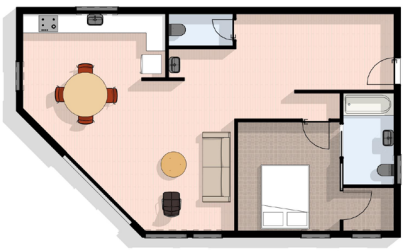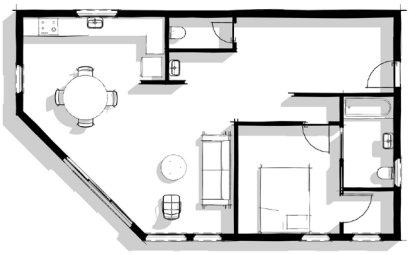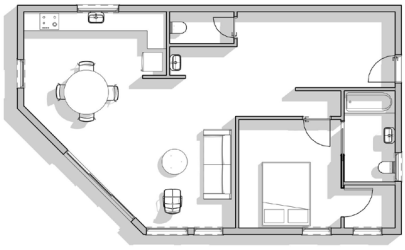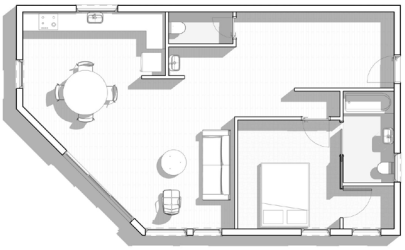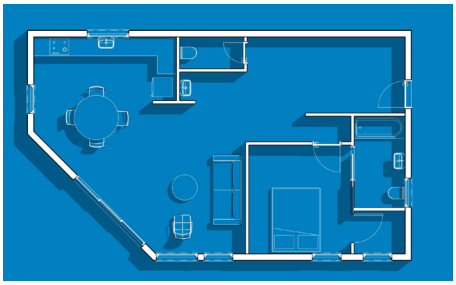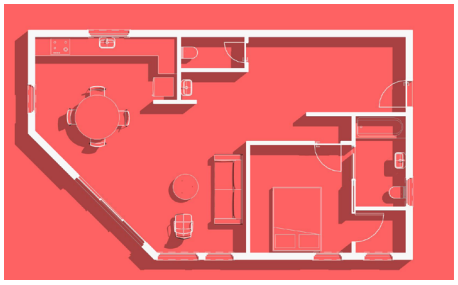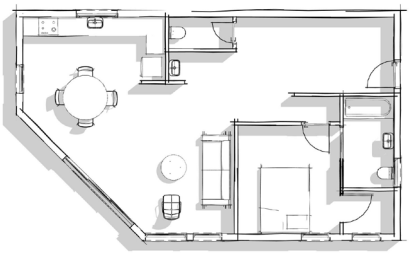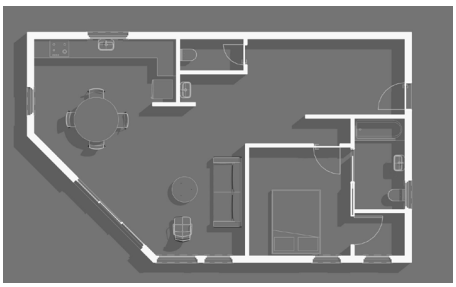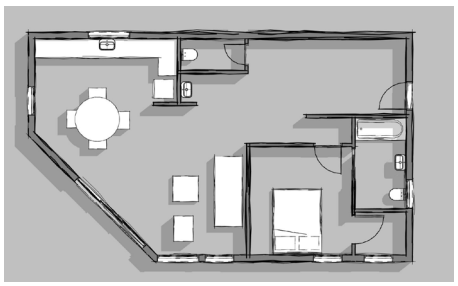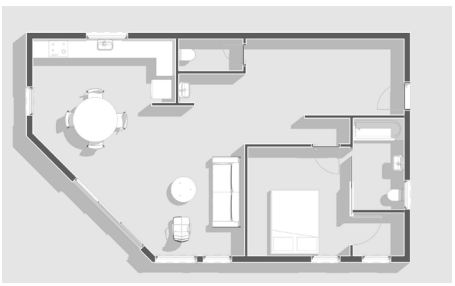View Template - פרזנטציה חתכים/חזיתות

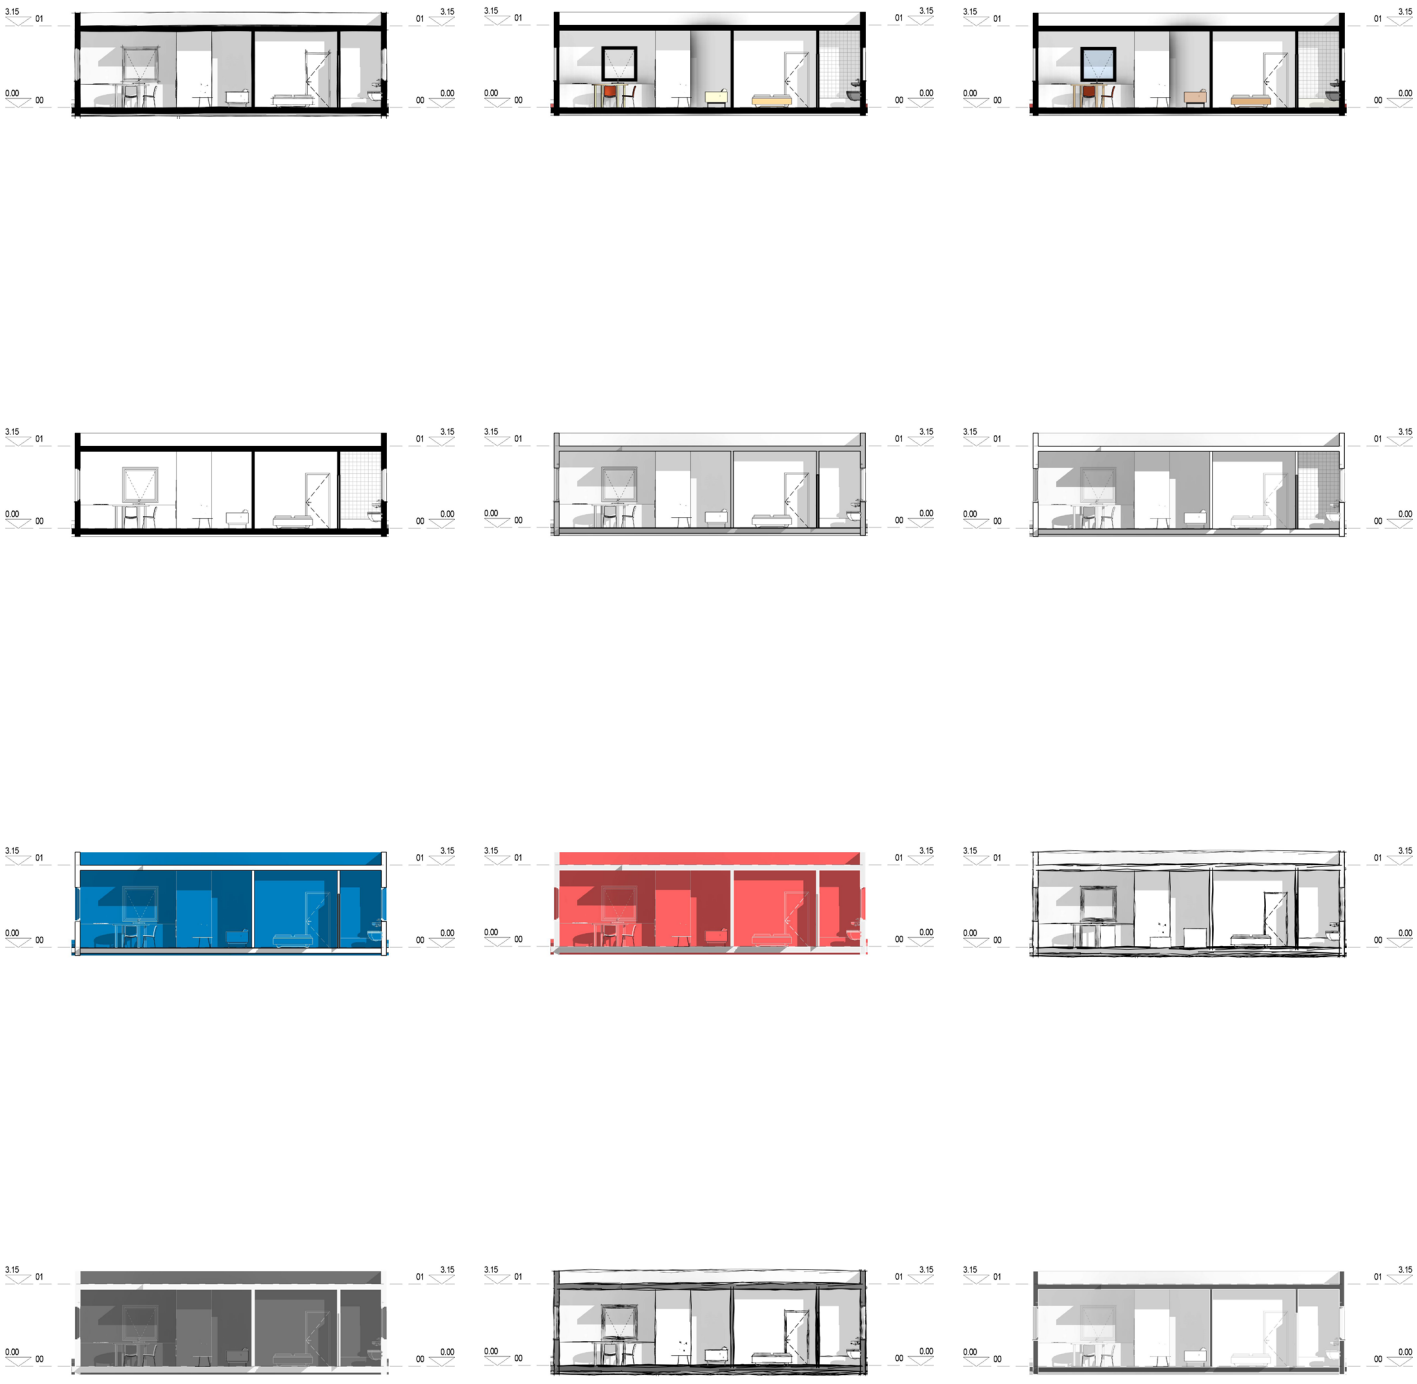


מה הטמפלט יודע לעשות ?

כל הזכויות שמורות לאלי שוקרי | איש אדריכלים בע"מ
www.ish.co.il | info@ish.co.il | 054-8811651


חומרים מוכנים מראש

לשימוש האישי שלכם


1. מעל 70 חומרים מוגדרים מראש עם פטרנים במבט בשחור לבן והצבע, חומר לריאליסטיק ורינדור

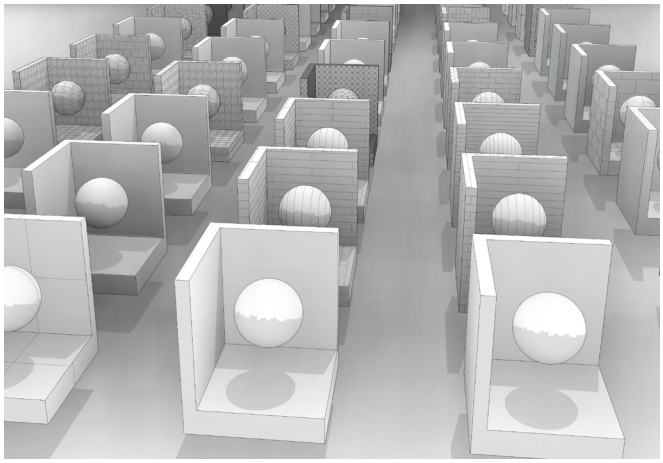


Hidden Line

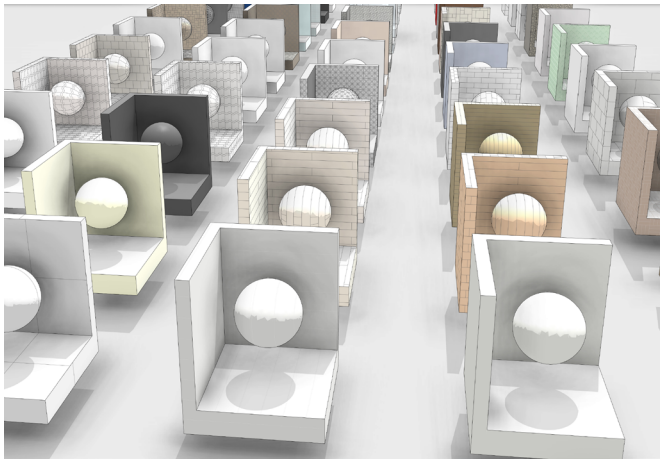


Shaded

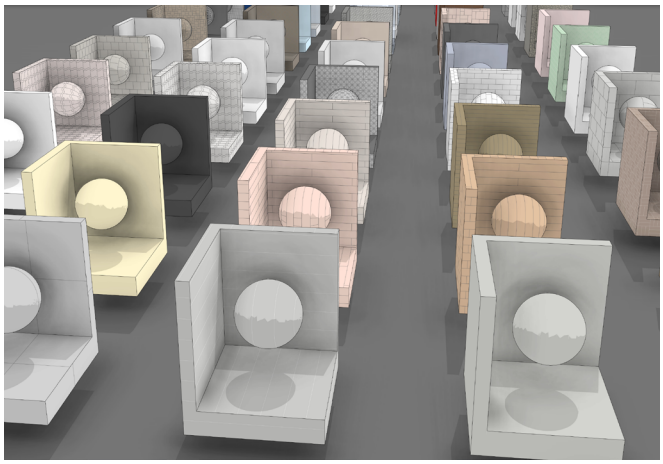

Consistent Color

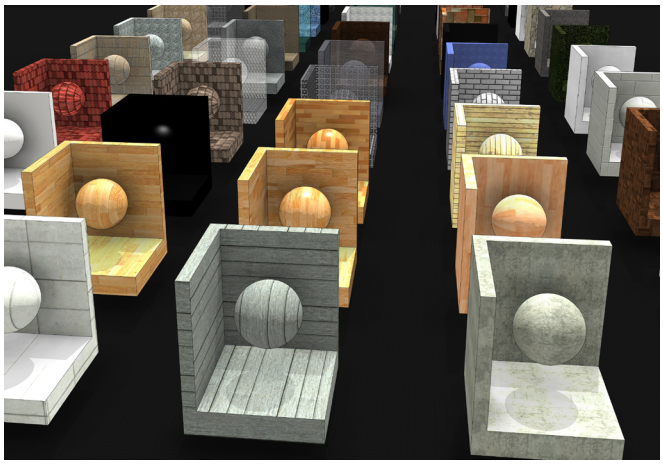

Realistic

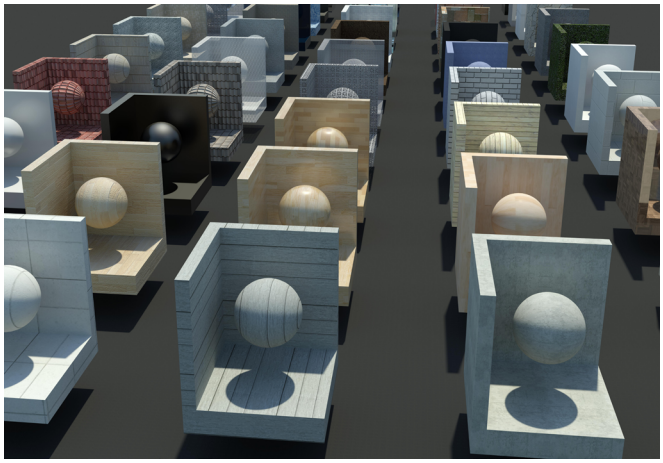

Render

כל הזכויות שמורות לאלי שוקרי | איש אדריכלים בע"מ
www.ish.co.il | info@ish.co.il | 054-8811651
ISH simple to know

Project Browser - סידור מסמכים

שיטה פשוטה נוחה ואטומטית לסידור הברואזר

שיטת סידור מבטים שתלווה אתכם בכל שלב של הפרוייקט, ותגרום לכם לעבוד מסודר ויעיל, ובעיקר לא לאבד מבטים בדרך מבלי לדעת איפה הם נמצאים.

2 רמות סידור כלליות:


1. לפי סיווג המסמך (תוכנית/חזית/חתך/תלת מימד וכו)
2. ואז לפי סוג המסמך (תוכניות ראשיות/פירוט שירותים/פירוט ח.מדרגות וכו)

כשפרוייקט מתפתח עוברים למצב של 3 רמות סידור על מנת לעבוד בנוחות מקסימלית

3. איגוד מבטים עם קידומת זהה

בנוסף עוד 2 אפשרויות לסידור הבראוזר בהתאם לשיטת העבודה של המשרד

4. 2 רמות סידור כנ"ל עם חלוקה לשלב בניה
5. 2 רמות סידור כנ"ל עם חלוקה לקנ"מ

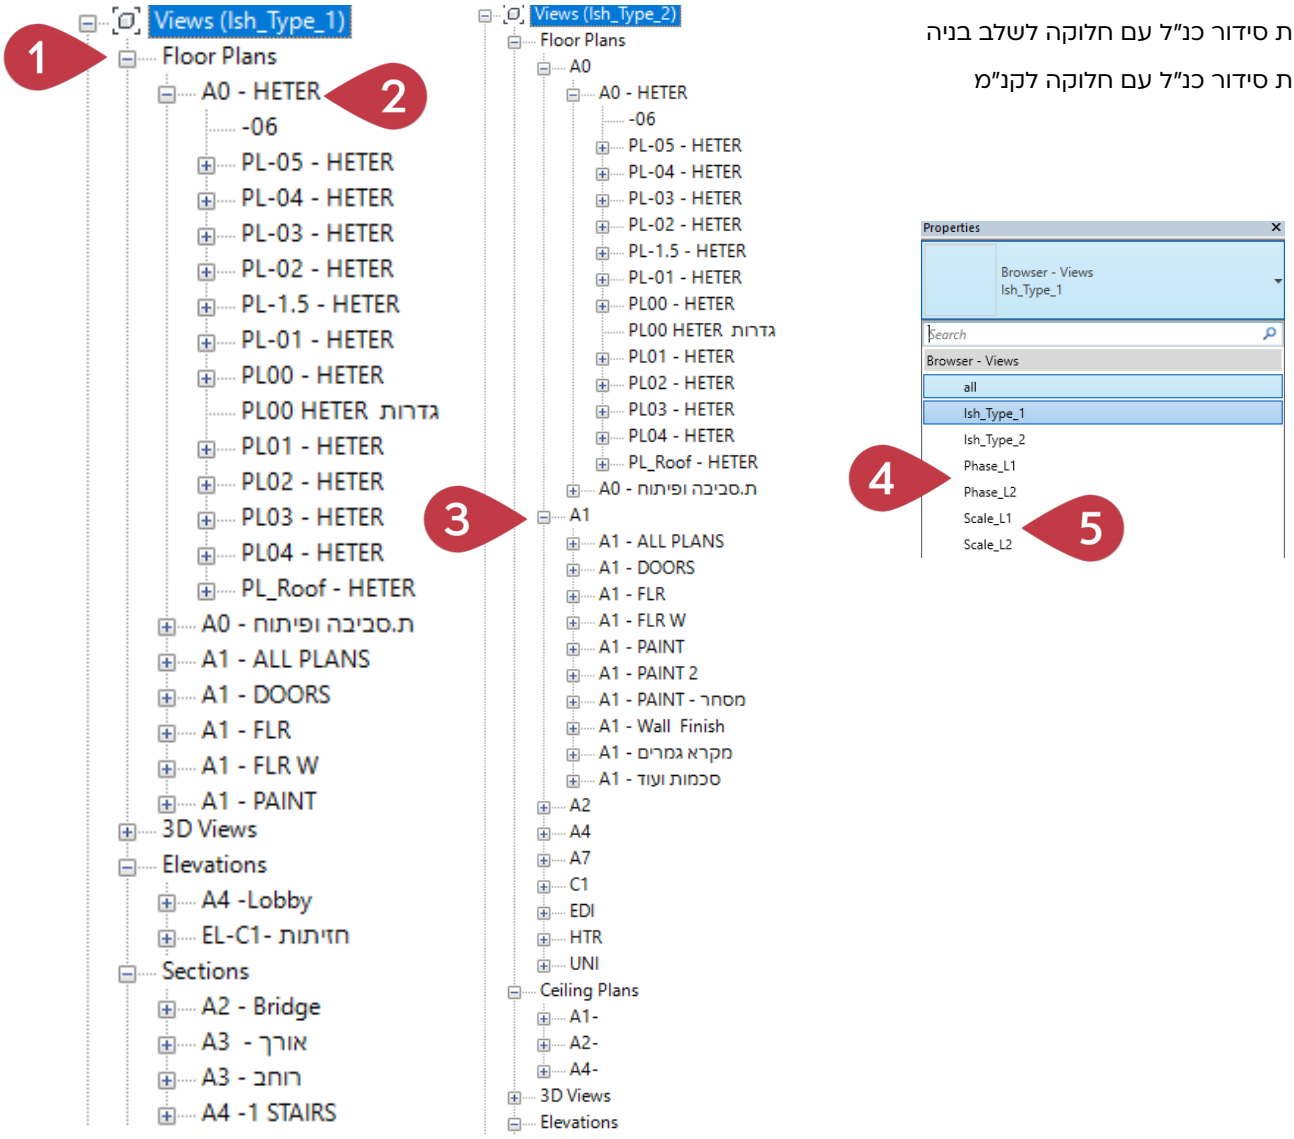


כל הזכויות שמורות לאלי שוקרי | איש אדריכלים בע"מ
www.ish.co.il | info@ish.co.il | 054-8811651
ISH simple to know

סימני חתכים

חתך מותאם לכל שימוש ומסווג את עצמו במקום המתאים

סימני חתכים - תצוגה לפי שימוש

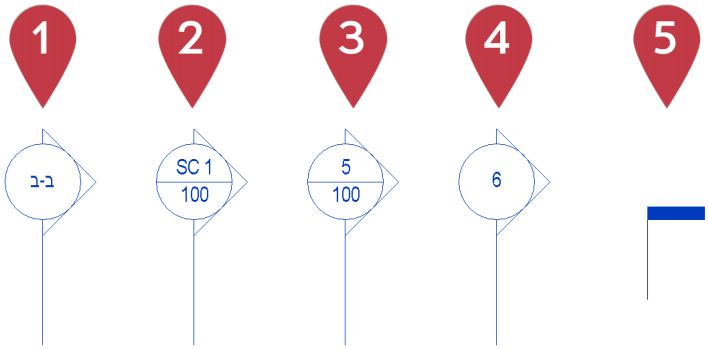


1. היתר - שם החתך
2. עבודה - שם החתך, מספר גליון
3. פירוטים - מספר מבט בגליון, מספר גליון
4. רשימות - מספר מבט בגליון
5. חתך עזר - זנב

חזיתות / פריסות

סימן חזית מותאם לכל שימוש ומסווג את עצמו במקום המתאים

סימני חזיתות - תצוגה לפי שימוש

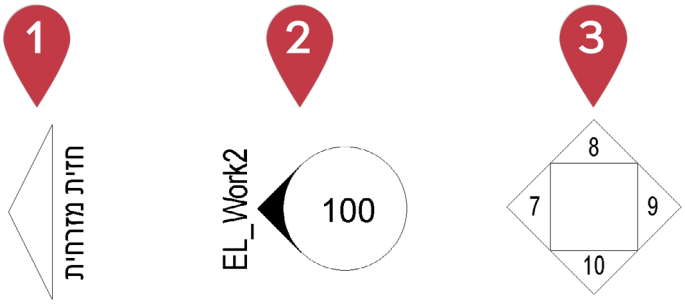


1. היתר - שם החזית (ללא מס' גליון)
2. עבודה - שם החזית + הפניה למספר גליון
3. פריסות - מספר כל פריסה על גבי הגליון

סימני גובה

לכל שימוש אפשרי

שלוש אפשרויות בתצוגת המידע

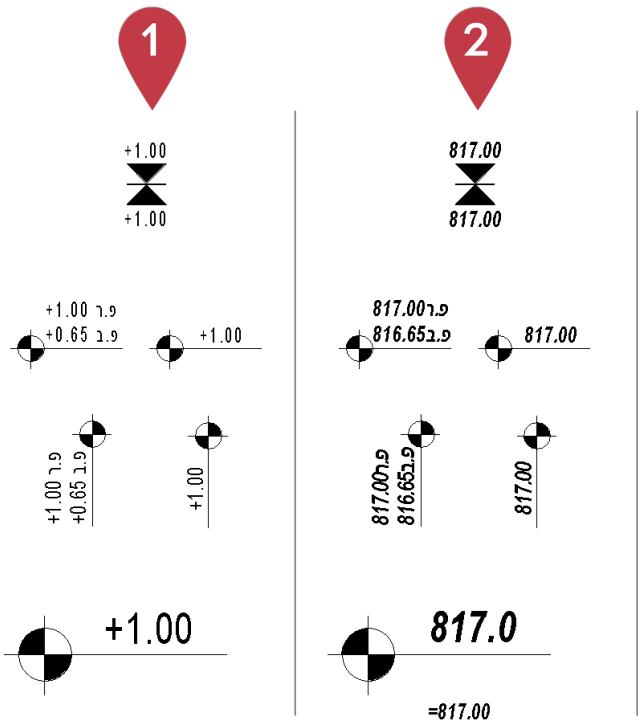

1. יחסי ל 00 של הפרוייקט
2. אבסולטי מגובה פני הים


לכל סוג מידע יש אייקונים בחזית (משולש עליון ותחתון) בתוכנית (אופקי ואנכי) ואייקון כפול בגודל לפרזנטציה

3. יחסי לקומה נבחרת ידנית

(להפרשי גובה בתוך הפרוייקט)

כל הזכויות שמורות לאלי שוקרי | איש אדריכלים בע"מ
www.ish.co.il | info@ish.co.il | 054-8811651
ISH simple to know


טקסטים

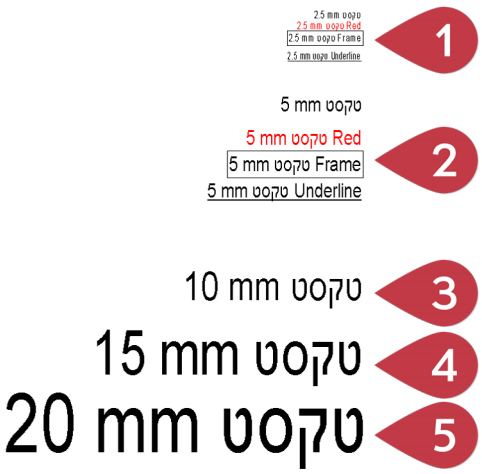

כל הגדלים כל הסוגים

1. 2.5 מ"מ (רגיל, אדום, ממוסגר, עם קו)
2. 5 מ"מ (רגיל, אדום, ממוסגר, עם קו)
3. 10 מ"מ
4. 15 מ"מ
5. 20 מ"מ


סימני שיפועים

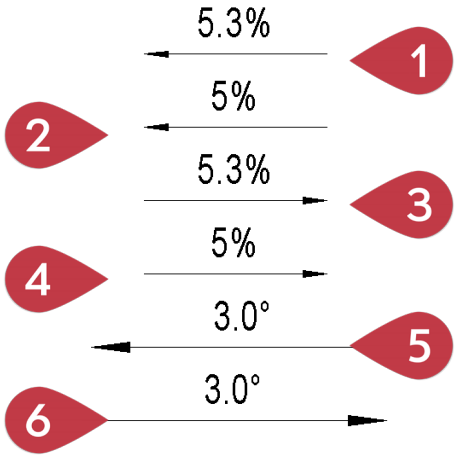

לפי הצורך

1. אחוזים נקודה עשרונית - ירידה
2. אחוזים מעוגל - ירידה
3. אחוזים נקודה עשרונית - עליה
4. אחוזים מעוגל - עליה
5. מעלות נקודה עשרונית - ירידה
6. מעלות נקודה עשרונית - עליה

קווי מידות

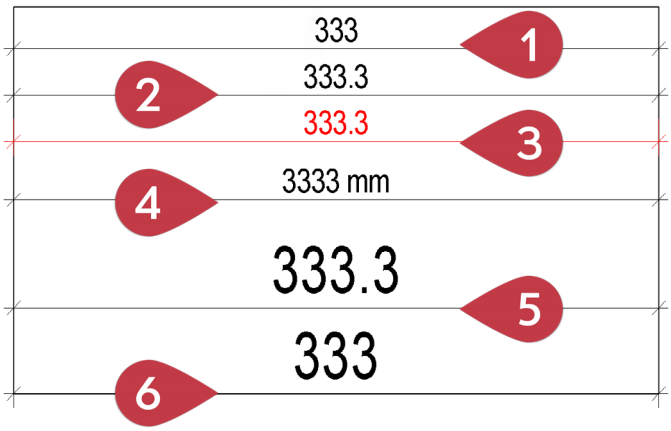


לפי הצורך

1. סנטימטרים מעוגל - 2.5 מ"מ
2. סנטימטרים נקודה עשרונית שחור - 2.5 מ"מ
3. סנטימטרים נקודה עשרונית אדום - 2.5 מ"מ
4. מילימטרים - 2.5 מ"מ (לפרטים)
5. סנטימטרים נקודה עשרונית שחור - 5 מ"מ (למצגת)
6. סנטימטרים מעוגל - 5 מ"מ (למצגת)

כל הזכויות שמורות לאלי שוקרי | איש אדריכלים בע"מ
www.ish.co.il | info@ish.co.il | 054-8811651
ISH simple to know


גרידים

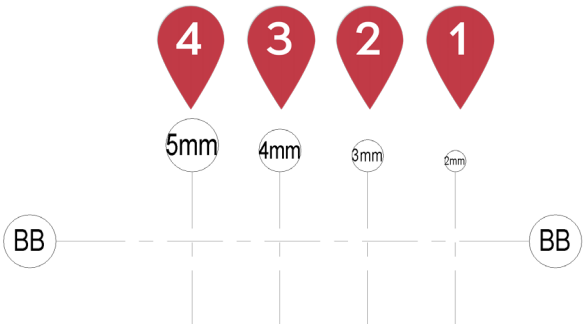

גדלים לבחירתכם

1. 2 מ"מ
2. 3 מ"מ
3. 4 מ"מ
4. 5 מ"מ


קווים

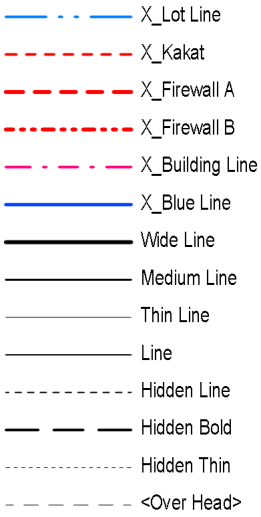

פשוטים לכל שימוש

- Hidden Thin- קוקו דק (Pen 1)
- Hidden Line - קוקו רגיל (Pen 3)
- Hidden Bold - קוקו מודגש(Pen 6)
- Thin Line- קו דק(Pen 1)
- Line- קו רגיל(Pen 3)
- Medium Line- קו בינוני(Pen 5)
- Wide Line - קו עבה(Pen 8)
- Kakat - קו קקט
- Building Line - קו בניין
- Lot Line - קו מגרש
- Blue Line - קו כחול
- FireWall A - קיר אש 1
- FireWall B- קיר אש 2

האצ'ים

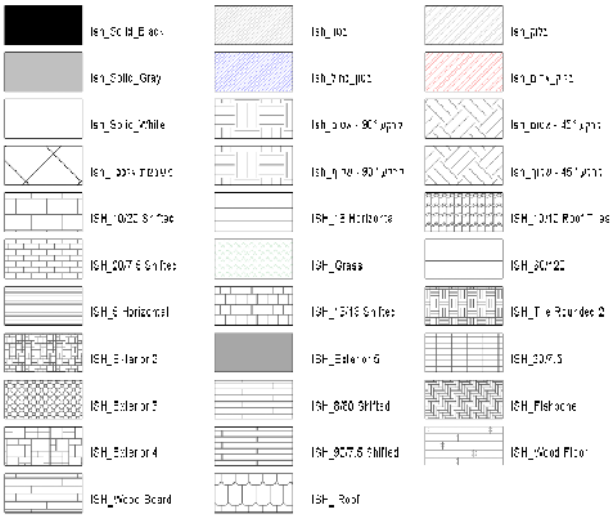


משמשים לחומרים ולריג'נים

-
- בלוק אדום
- בלוק שחור
- בטון כחול
- בטון שחור
- אדמה 45 מעלות
- אדמה 90 מעלות
- סוליד לבן
- סוליד אפור
- רעפים
- ועוד


כל הזכויות שמורות לאלי שוקרי | איש אדריכלים בע"מ
www.ish.co.il | info@ish.co.il | 054-8811651
ISH simple to know

גליונות - Title Blocks

כל הגדלים, גמיש וחכם

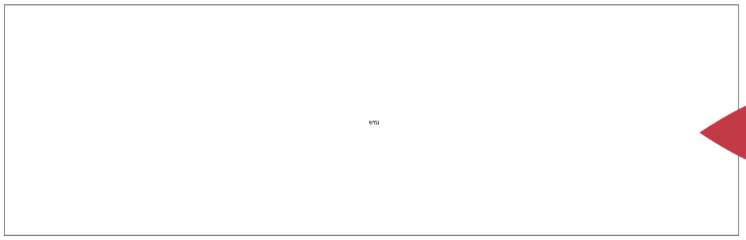



1. גובה ואורך גמיש להיתר
2. A0, A1,A2 - סטריפ משרדי חכם (הרחבה בהמשך)
3. A3,A4 עומד ושוכב עם סטריפ מקוצר
4. גליון שער לרשימות

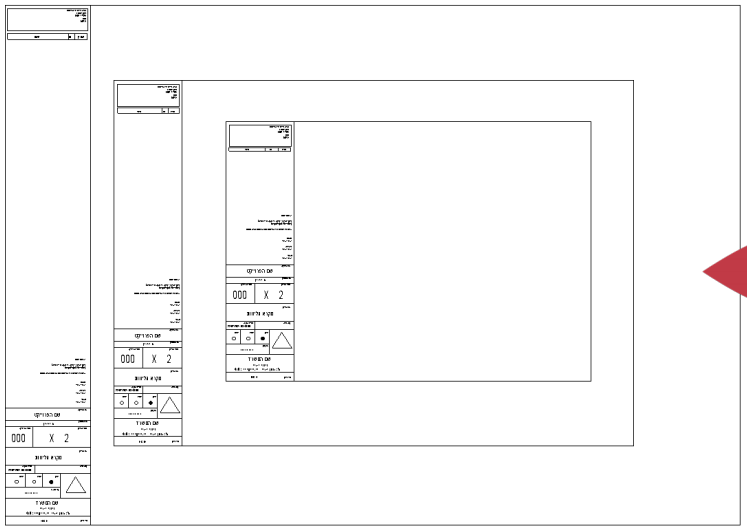


אפשרויות בגליונות A0,A1,A2

- גובה קבוע אורך משתנה גמיש
- הצגת תאריך מהדורה אוטומטי או ידני
- הצגת מספר מהדורה אוטומטי או ידני
- שינוי סימון סטטוס עיון/מכרז/ביצוע
- הצגת קנ"מ אוטומטי או ידני (כשיש מספר קני מידה לא מוצג טקסט אוטומטי)
- רשימת יועצים מתעדכנת בכל הגליונות
- הערות קבועות בראש הגליון
- חץ צפון פרמטרי
- רשימת תפוצה עם מנגנון נח להזנה (אופציונלי)
- טבלת שינויים בהתאם למהדורות מובנות ברוויט
- פרטי המשרד
- תאריך ושעת הפצה (אי אפשר להוריד את השעה נכון לזמן כתיבת החוברת הזו)

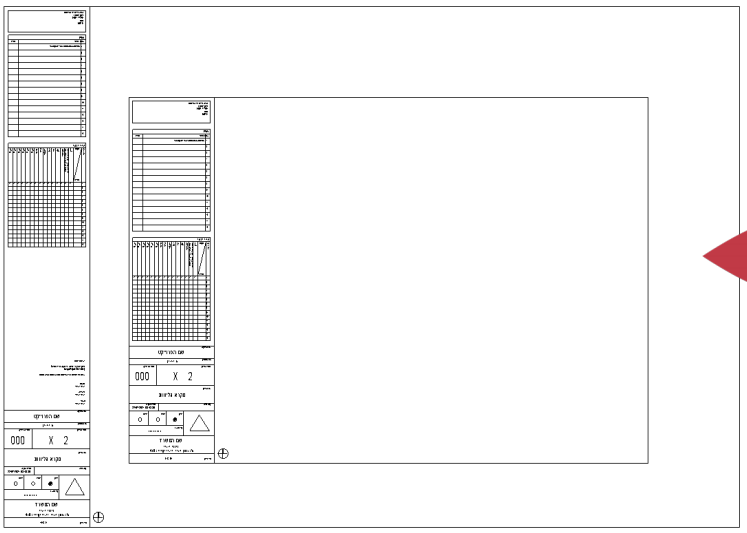

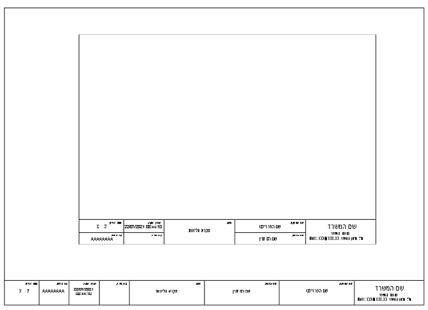

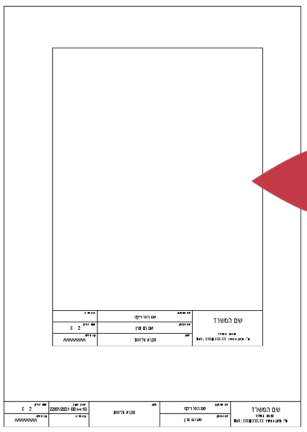



כל הזכויות שמורות לאלי שוקרי | איש אדריכלים בע"מ
www.ish.co.il | info@ish.co.il | 054-8811651
ISH simple to know

כותרות למבטים בגליונות

שמאל ימין ווריאציות שונות לפי צורך

- שילובים של שם המבט, קנ"מ ו Detail Number
- ימין או שמאל
- עם קו ובלי קו

2 קומת קרקע
1 : 50

2 קומת קרקע
1 : 50

קומת קרקע
1 : 50

2 קומת קרקע
1 : 50

קומת קרקע
1 : 50

קומת קרקע

קומת קרקע
1 : 50


קומת קרקע

טבלאות

מוכנות מראש רק לבנות פרוייקט

טבלאות הן כלי עוצמתי מאוד ברוויט, עם הכנות נכונות של טבלאות שטף העבודה הופך להיות מקצועי יותר ומהיר

- סכמות שטחים
- דלתות
- מפלסים
- רשימות (+ מנגנון סיווג רשימות כדי לא לפספס אלמנטים)
- מהדורות לפי פמלי מיוחד
- חניות
- ROOMS
- גליונות
- מבטים
- קירות
- חלונות
- טבלאות ריקות לשימוש חופשי
- חומרים ברצפות
- חומרים בקירות
- ריכוז הערות
- מעקות
- ועוד...

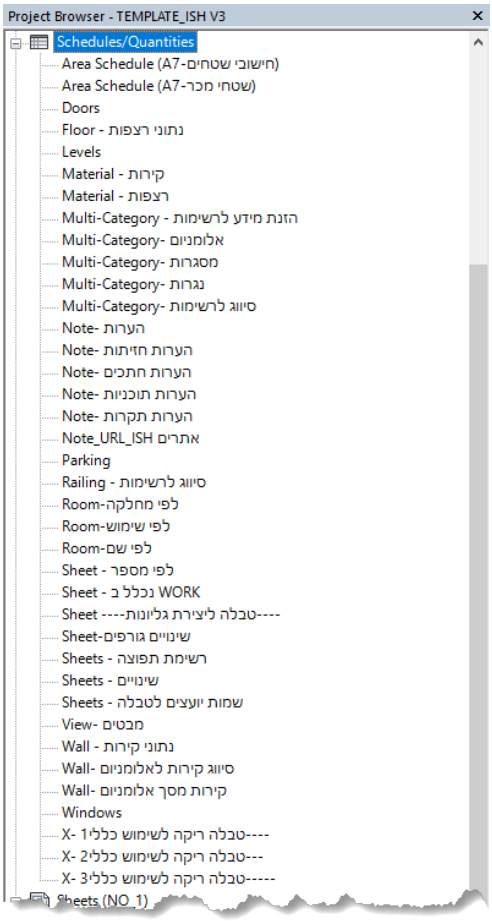


כל הזכויות שמורות לאלי שוקרי | איש אדריכלים בע"מ
www.ish.co.il | info@ish.co.il | 054-8811651
ISH simple to know

Phasing - שלביות ביצוע

הכנות לכל אפשרות


להכנת תוכניות בשלביות ביצוע כמו מצב קיים, הריסה, בניה חדשה ובניה עתידית,
באפשרויות שונות לתצוגה ובגרפיקה לפי המקרא הנ"ל. (ללא יצירת קירות בגרפיקות שונות,
זו פקודה מובנית ברוויט שעושה את הכל)

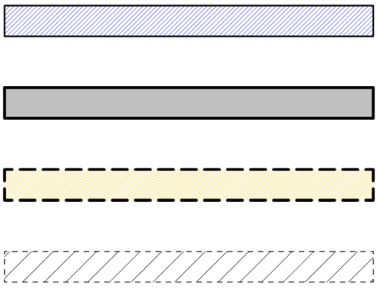


פילטרים לתצוגת שלבים:

- קודם + נוכחי
- קודם + נוכחי בלי פליטר
- קודם
- קודם + הריסה
- נוכחי
- נוכחי + הריסה
- נוכחי + זמני
- הריסה
- נוכחי כעתידי


דוגמה לסט תוכניות אפשרי

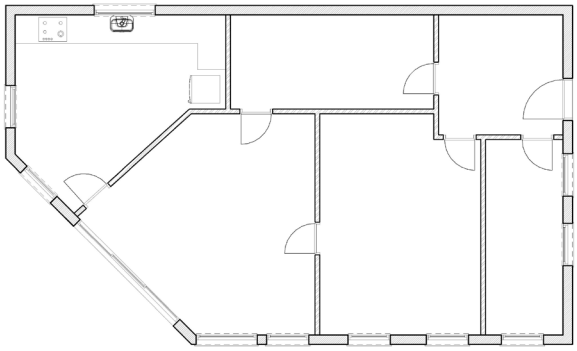


01 - מצב קיים

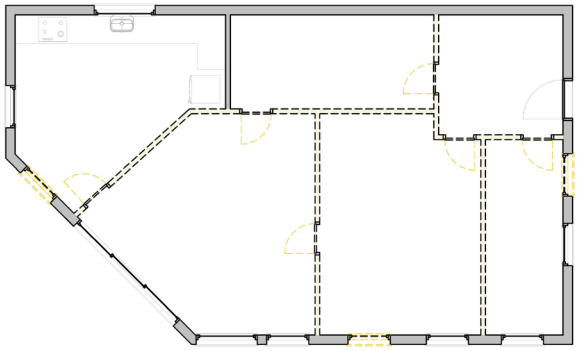

02 - הריסה

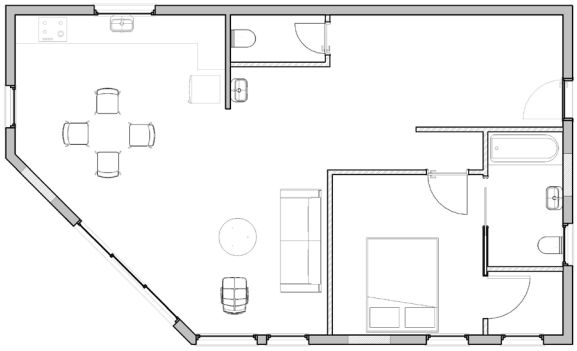

01 - מצב חדש

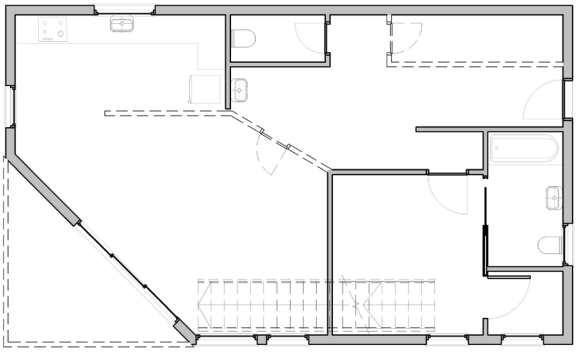

02 - תכנון עתידי

כל הזכויות שמורות לאלי שוקרי | איש אדריכלים בע"מ
www.ish.co.il | info@ish.co.il | 054-8811651


ROOMS - פרמטרים, סכמות צבע וטאגים

גמישות בהצגת המידע


קיימים 4 פרמטרים (שם, מחלקה, שימוש, שימוש למצגת) בעזרתם אפשר לצבוע תוכניות באופן אוטומטי ולהם כבר מוכנים סכמות צבע, רק לבחור ולהזין את הפרמטרים הרצויים על מנת להציג את המידע כמו שאתם רוצים, על גבי אותה תוכנית בוריאציות שונות.

בנוסף טאג יעודי שמציג כל וריאציה אפשרית של המידע הנ"ל בתופסת שטח
+ טאג כפול בגודל לטובת מצגת

1. פרמטרים יעודיים
2. טאג שמציג את הפרמטרים
3. סכמות צבע לפי הפרמטרים

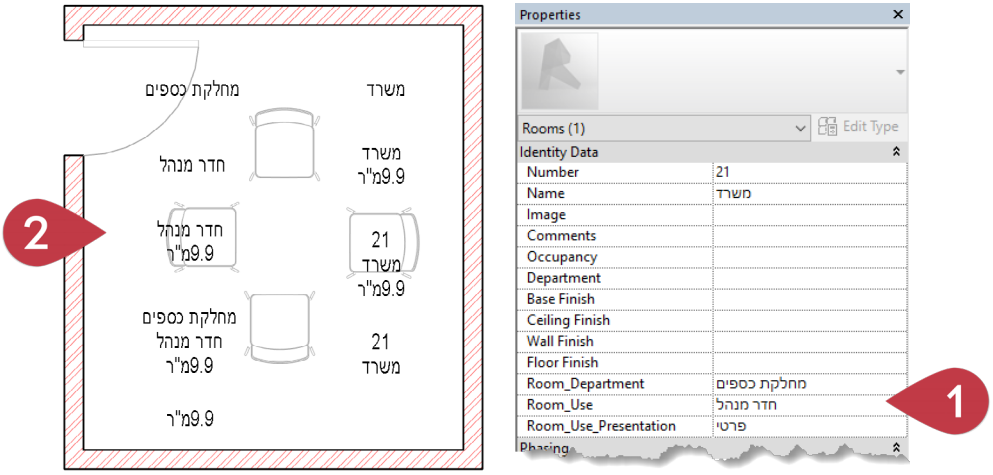

דוגמאות לאפשרויות צביעה שונות באופן אוטומטי ע"י ROOMS

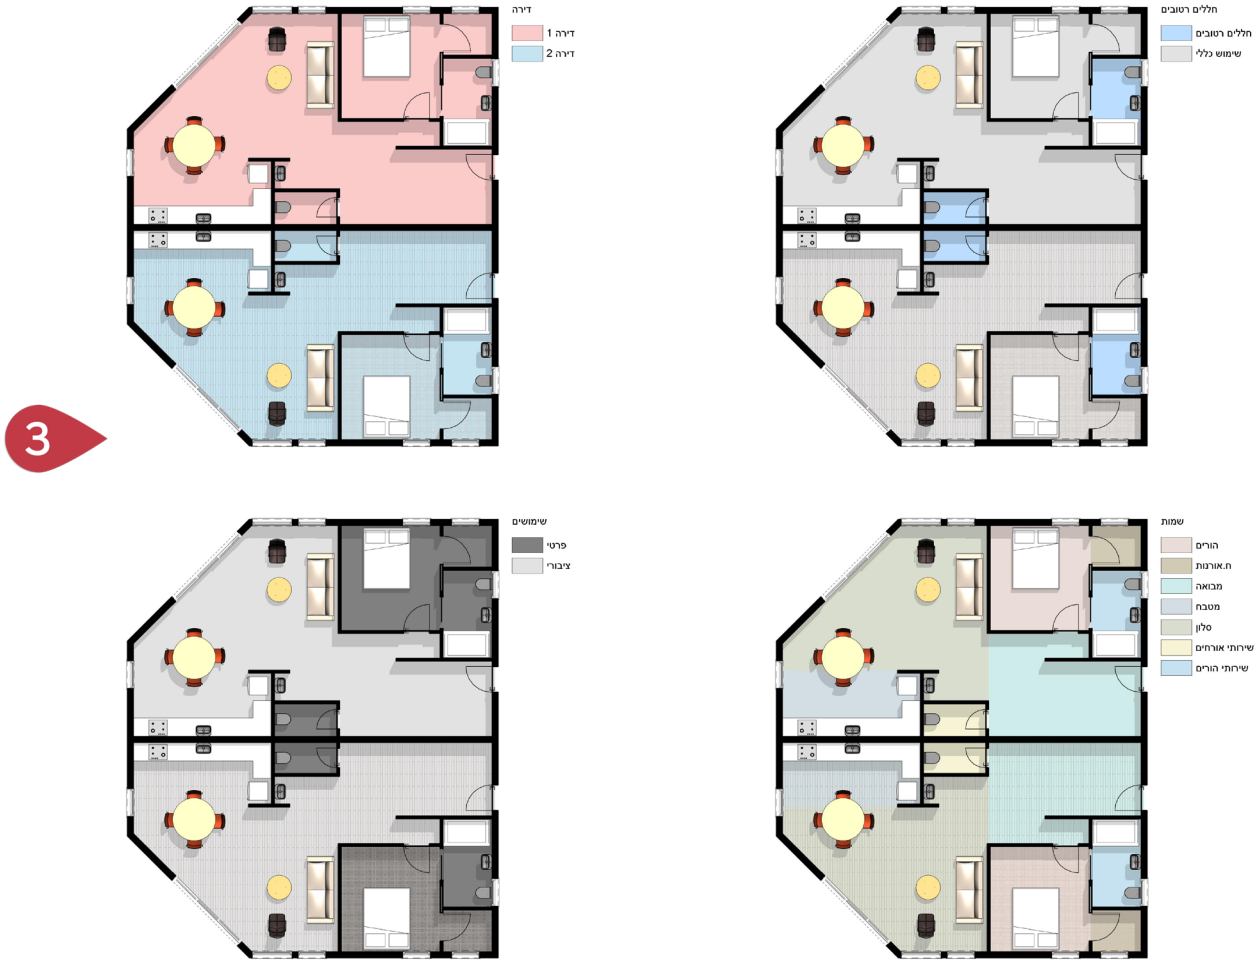


AREA - פרמטרים, סכמות צבע וטאגים


גמישות בהצגת המידע

קיימים 3 פרמטרים (שם, מחלקה, שימוש) בעזרתם אפשר לצבוע תוכניות באופן אוטומטי ולהם כבר מוכנים סכמות צבע, רק לבחור ולהזין את הפרמטרים הרצויים על מנת להציג את המידע כמו שאתם רוצים, על גבי אותה תוכנית בוריאציות שונות.


בנוסף טאג יעודי שמציג כל וריאציה אפשרית של המידע הנ"ל בתופסת שטח
+ טאג כפול בגודל לטובת מצגת


1. פרמטרים יעודיים
2. טאג שמציג את הפרמטרים
3. סכמות צבע לפי הפרמטרים

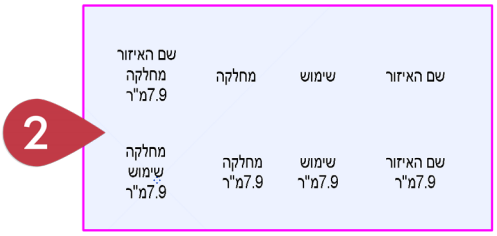

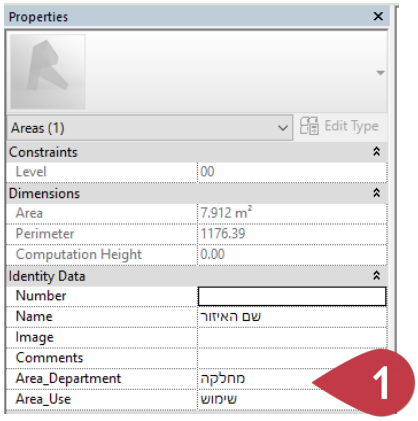


דוגמאות לאפשרויות צביעה שונות באופן אוטומטי ע"י AREA

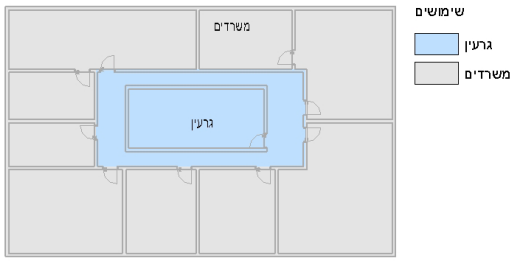

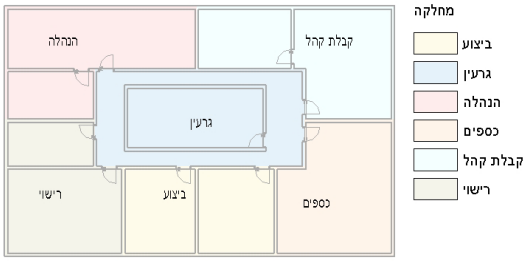

3

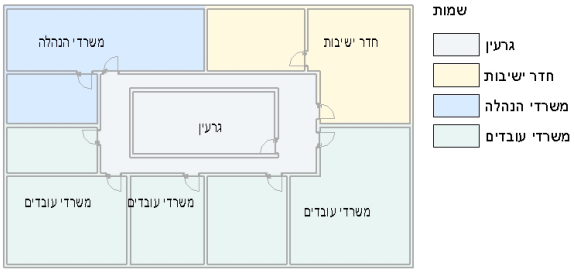


כל הזכויות שמורות לאלי שוקרי | איש אדריכלים בע"מ
www.ish.co.il | info@ish.co.il | 054-8811651
ISH simple to know

טאגים

לעבוד חכם


אחת הדרכים היעילות לחסוך זמן ולהמנע מטעויות הוא שימוש בטאגם שקוראים נתונים מתוך האובייקטים אותם הם מתייגים. בטמפלט תמצאו טאגים מוכנים מראש למגוון שימושים

Multy Category Tag - כללי

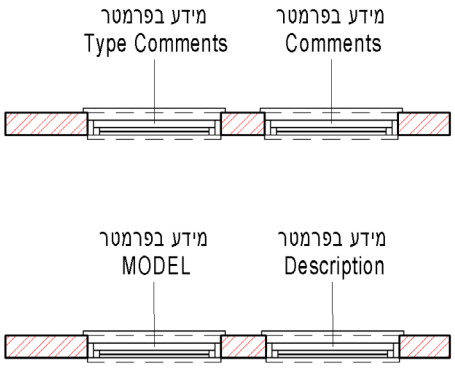


1. Comments
2. Type Comments
3. Model
4. Description

Multy Category Tag - סימון רשימות

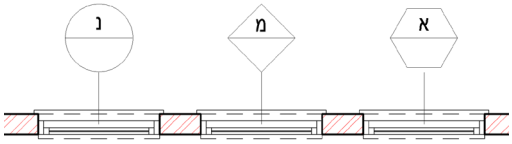

ע"פ פרמטר מיוחד, וסיווג בעזרת טבלה ייעודית על מנת לא לפספס אלמנטים (עדיין צריך לתייג בכל המסמכים, אבל גם אם מפספסים הטבלה תיהיה מעודכנת)

Multy Category Tag - טאג דף רשימה

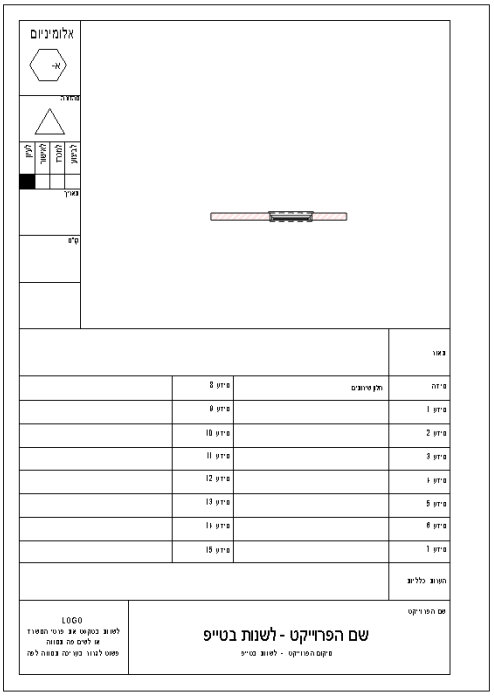


המציג נתונים מתוך האובייקט עצמו, ניתן להזין מראש לאובייקטים השונים את כל הנתונים (כמו זיגוג, פרזול, הערות וכל דבר בעצם) לערוך את הטאג בהתאם לשימוש המשרד.

את הנתונים אפשר להזין לכל פריט בנפרד או ע"י טבלה מרכזת המוכנה מראש

על גבי הגליון יש למקם את המבטים הרצויים של הפריט.

מה הטמפלט יודע לעשות ?


טאג דלתות

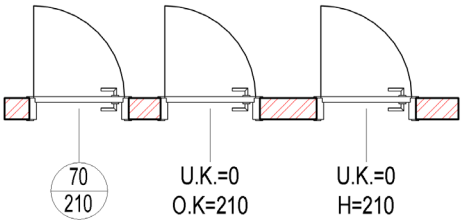


1. רוחב + גובה בעיגול
2. =UK= OK
3. =UK= H

טאג חלונות




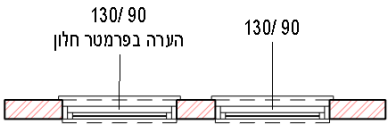

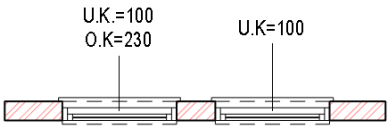


1. שם
2. שם + הערה
3. רוחב + גובה
4. רוחב+ גובה + הערה
5. =UK
6. =UK= OK

טאג צנרת

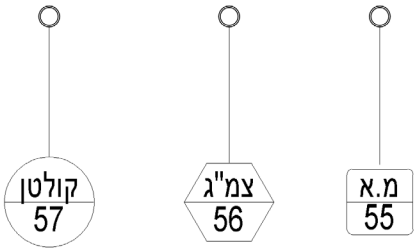

1. קולטן
2. צמג
3. מ.א

טאגי מדרגות

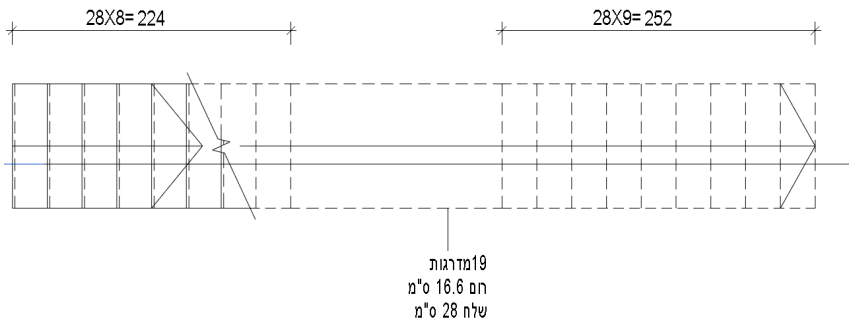


1. מספר מדרגות, גובה רום, אורך שלח
2. מספר שלחים X אורך שלח (לתוכנית)
3. מספר רומים X גובה רום (לחתך)

כל הזכויות שמורות לאלי שוקרי | איש אדריכלים בע"מ
www.ish.co.il | info@ish.co.il | 054-8811651
ISH simple to know


טאג חומרים

1. שם חומר
2. תיאור חומר
3. תיאור + הערה בחומר

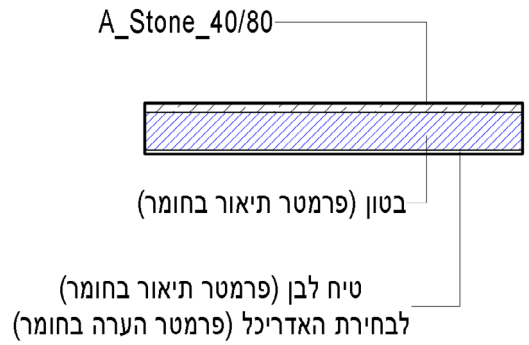


טאג ענני מהדורות

1. מספר מהדורה
2. מספר מהדורה + הערת ענן
3. מספר מהדורה + הערת ענן + מספר הערה

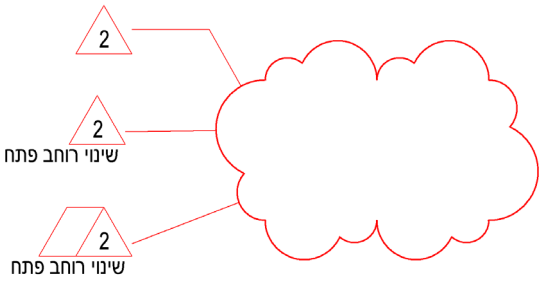


טאג מאסות


1. שם מאסה + נפח (טוב למאגרי מים)

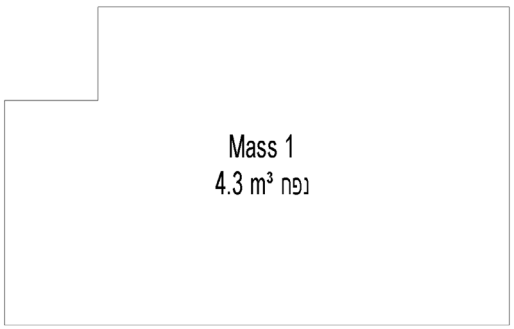

טאגים נוספים

1. קירות - תיאור / TYPE MARK
2. רצפות - תיאור / TYPE MARK
3. מעקות
4. עמודים
5. KEYNOTE
6. מספור חניות

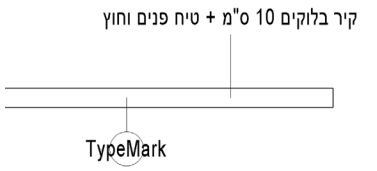

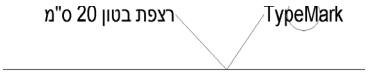

כל הזכויות שמורות לאלי שוקרי | איש אדריכלים בע"מ
www.ish.co.il | info@ish.co.il | 054-8811651
ISH simple to know

3

קטלוגים

קטלוגים

קטלוג זה בעצם קובץ פרוייקט ללא פרוייקט, שמכיל בתוכו את האלמנטים שלכם פרוסים על גביו כדי פשוט להכנס ולקחת, ממש כמו לבחור מקטלוג. ויהיו בו בעצם כל הדברים שאנחנו משתמשים בהם לאורך חייו של פרוייקט. כמו, חלונות, דלתות, רהיטים, קירות, רצפות וכו.


למה שהם לא יהיו מההתחלה בטמפלט ?


פרוייקט מתקיים לאורך זמן רב, ועדיף שהקובץ יכיל רק דברים שאנחנו באמת צריכים ולא יהיה עמוס וכבד מידי. אם נזין את כל הקטלוג שלנו עם המון סוגי חלונות, והמון סוגי דלתות וכו, הקובץ יהיה כבד מאוד וזה עוד לפני שקיים בכלל פרוייקט.


לכן בטמפלט נכניס רק אלמנטים הכרחיים בלבד להתחלה של פרוייקט ואלמנטים שלא מכבידים במיוחד (כמו סוגי מידות וטאגים למשל) וככל שהפרוייקט מתקדם נאסוף אלמנטים חדשים מתוך הקטלוג לפרוייקט שלנו.

מה מצורף לטמפלט

1. קטלוג ISH- הפורס את כל האלמנטים של הטמפלט ומעבר
2. קטלוג משפחות מתוך אתר BIM OBJECTS
3. קטלוג משפחות מתוך ספריות AUTODESK

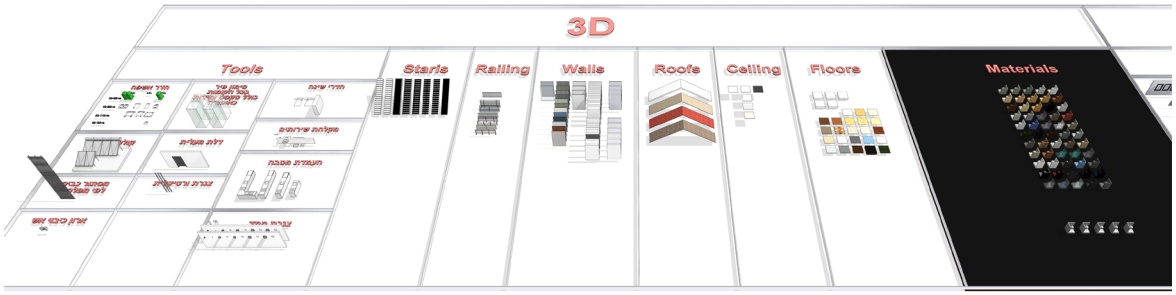

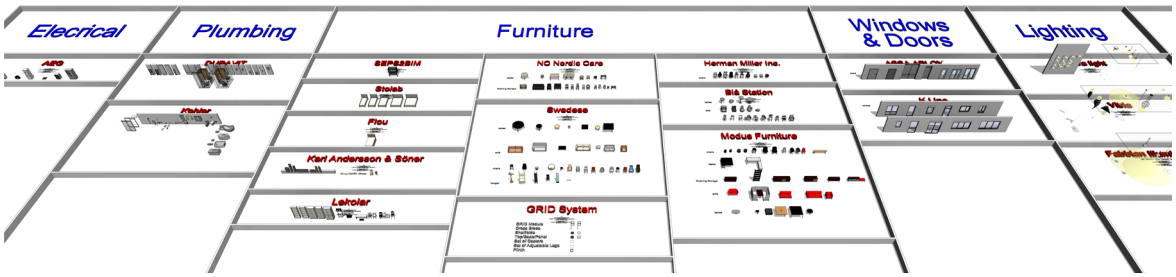

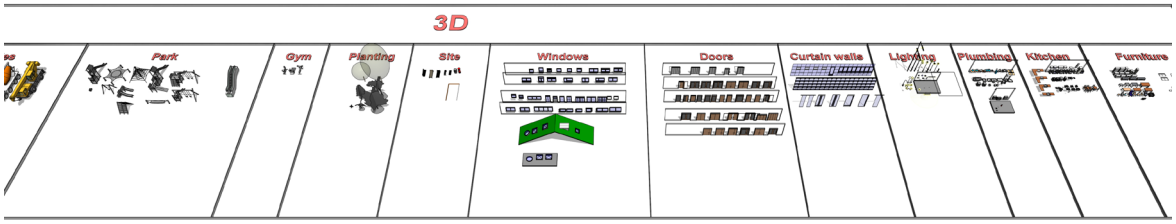


כל הזכויות שמורות לאלי שוקרי | איש אדריכלים בע"מ
www.ish.co.il | info@ish.co.il | 054-8811651
ISH simple to know


קטלוג ISH


כל האלמנטים שמוגדרים בטמפלט פורסים כאן, טאגים, סוגי טקסטים,סוגי חתכים, חזיתות, גרידים, על מנת לאפשר לערוך את הטמפלט הראשי מבלי לאבד מידע ולשמר אותו במקום אחד מרוכז


בנוסף ! מספר אלמטים שבנינו במיוחד לרוכשי הטמפלט


1. סוגי קירות
2. סוגי רצפות
3. סוגי גגות
4. סוגי מדרגות

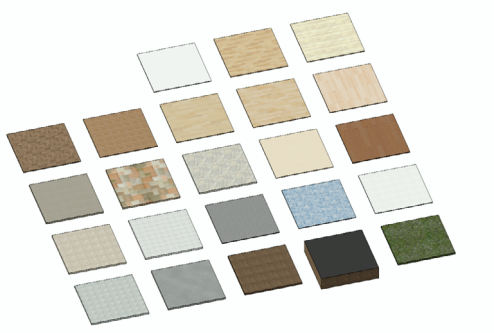

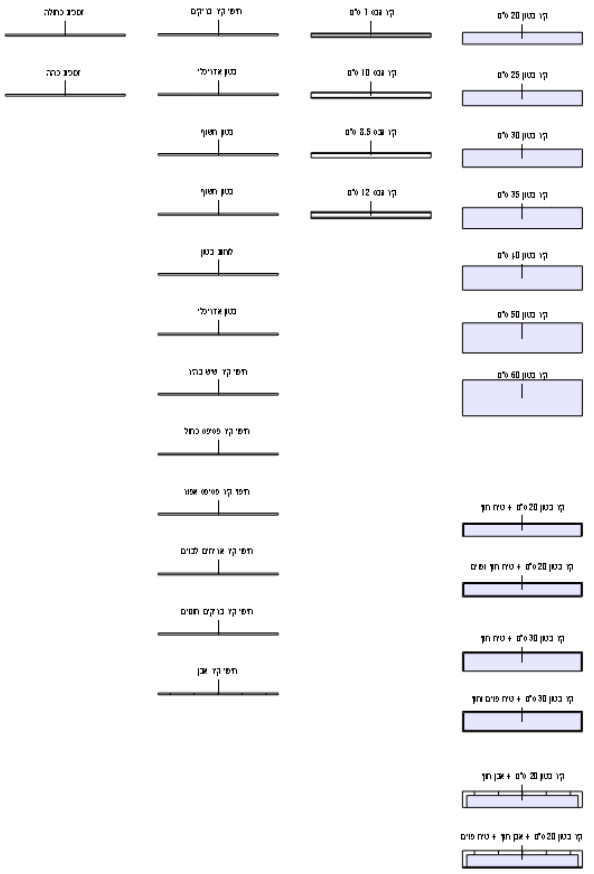

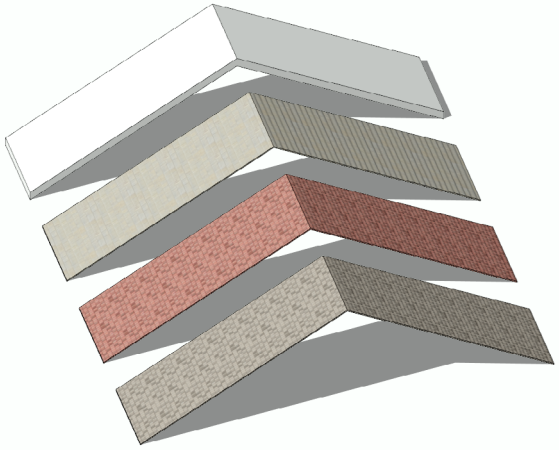


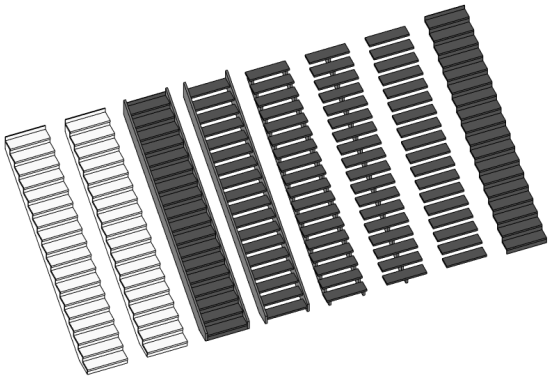

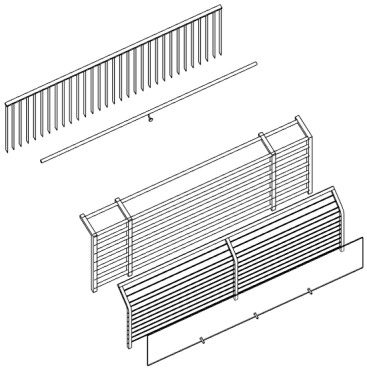

כל הזכויות שמורות לאלי שוקרי | איש אדריכלים בע"מ
www.ish.co.il | info@ish.co.il | 054-8811651

סימן פיר שמופיע בכל הקומות

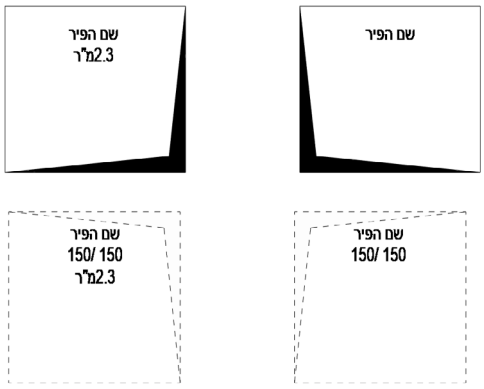


פמלי של פיר, נמתח, אליו מזינים את גובה הפיר לפי מפלסי הפרוייקט, ובכל תוכנית שהפיר חותך אותה מופיע סימן פיר, כולל טקסט לבחירה אוטומטי

1. שם
2. שם ושטח
3. שם ומידות
4. שם מידות ושטח
5. ללא טקסט


כשהפיר נמצא מעל החיתוך בטווח התוכנית הוא יופיע כמקוקוו

משפחות למטבח גנרי

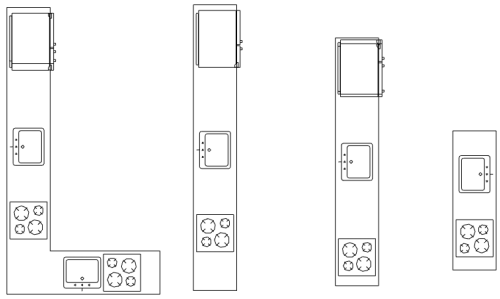


ניתן למתיחה ולהזזה נוחה של האובייטים השונים (גז, כיור, מקרר)

ארון גמיש

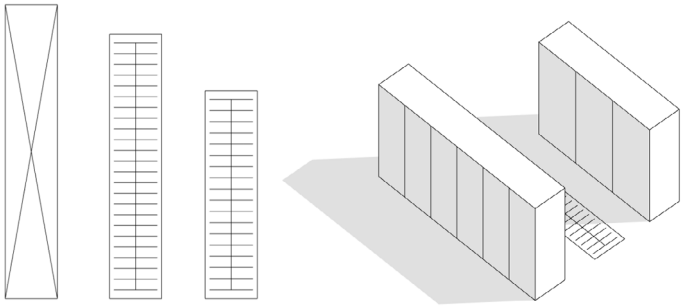

1. נמתח לכל כיוון (אורך, רוחב, גובה)
2. אפשרות להציג קווים (קולבים) או איקס
3. אפשרות להזין מספר חלוקות גנריות בחזית
4. אפשרות הצגה בתלת מימד או ללא הצגה

אשפה

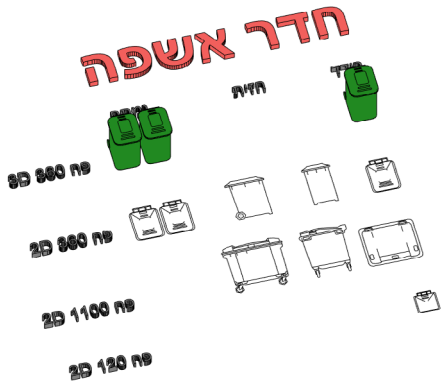

פחים בתוכנית וחזית

מה הטמפלט יודע לעשות ?


כל הזכויות שמורות לאלי שוקרי | איש אדריכלים בע"מ
www.ish.co.il | info@ish.co.il | 054-8811651
ISH simple to know

פמלי הערות

לכל הערה יש פרמטרים משלה כמו מספר,תאריך, למי מיועדת הערה ועוד.


בנוסף כל הערה מתועדת אוטומטית בטבלה ייעודית מוכנה מראש, כולל סיווג הערות למסמכים או אנשים.

וככה אפשר לנהל את הערות בקלות

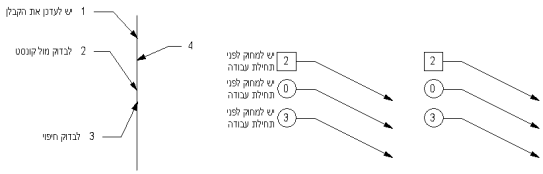

פמלי מידות מכר

פמלי דו מימד, שנראה כמו מידה רגילה לגמרי ובו יש פרמטר שאפשר לבחור איזה ערך להוריד מהמידה המקורית.

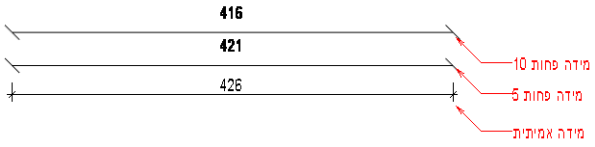

פמלי חישוב שיפוע

פמלי דו מימד, מזינים גובה התחלתי ואחוז שיפוע ומקבלי את הגובה הסופי



פמלי קישורים

מזינים קישור לתקיית הפרוייקט במחשב, קישור לאתר מסויים או קישור למסמך מסויים, ובלחיצה על הפמלי הוא ישגר אתכם לשם בלי לחפש יותר מידי




פמלי סימון איזור

סימון איזורים מסויימים מצד לצד ע"י טקסט. מצויין לפרזנטציות

כל הזכויות שמורות לאלי שוקרי | איש אדריכלים בע"מ
www.ish.co.il | info@ish.co.il | 054-8811651
ISH simple to know

פמלי סימון רמפה

דו מימד, נמתח, כדי לסמן רמפות בתוכניות.

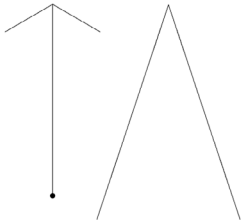


פמלי סימון קווי בטון בחזית

דו מימד פרמטרי, מזינים את עובי הבטון מדביקים בחזית ומקבלים את הסימון הרצוי בלי קווים מיותרים.




פמלי סימון אזורים

דו מימד נמתח, אופציות להוספת טקסטים בכל פאה

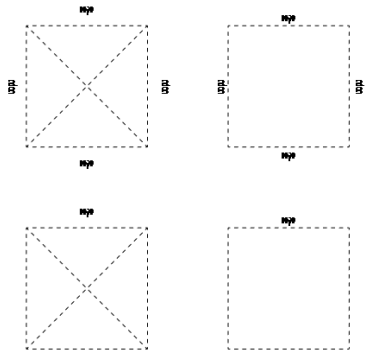


פמלי דמויות

דו מימד, אנשים לחזיתות

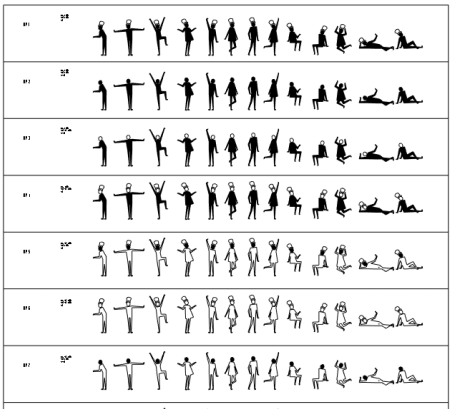

פמלי דף ראשון

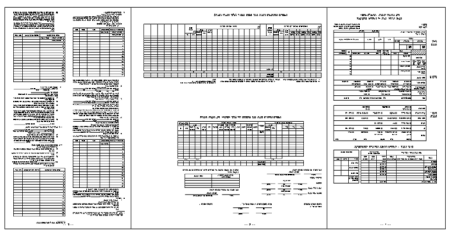


כל הזכויות שמורות לאלי שוקרי | איש אדריכלים בע"מ
www.ish.co.il | info@ish.co.il | 054-8811651
simple to know


קטלוג מתוך אתר BIM OBJECTS


1. חלונות
2. דלתות
3. תאורות
4. רהיטים
5. מוצרי חשמל
6. ברזים
7. כיורים
8. ועוד







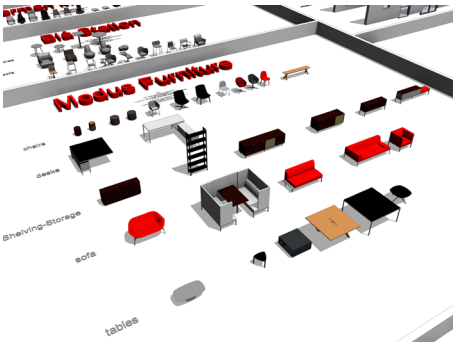


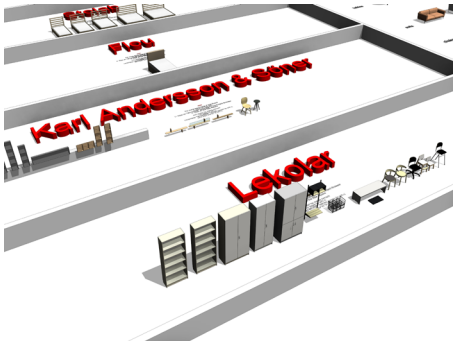


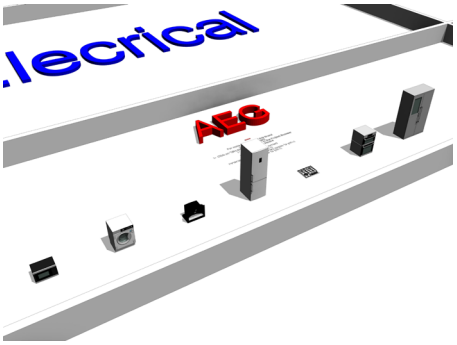


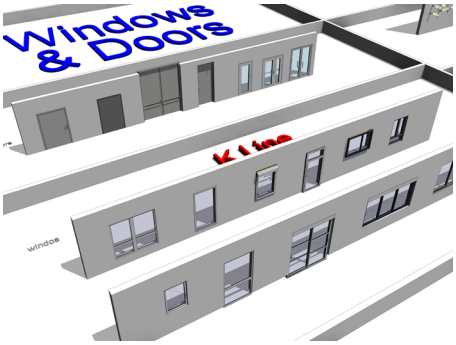


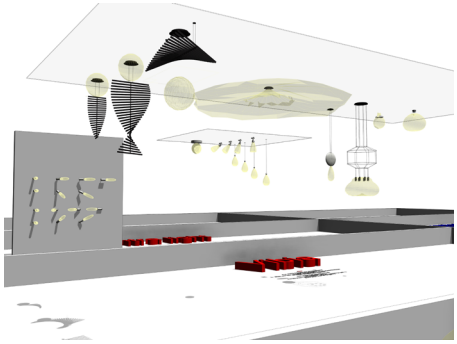


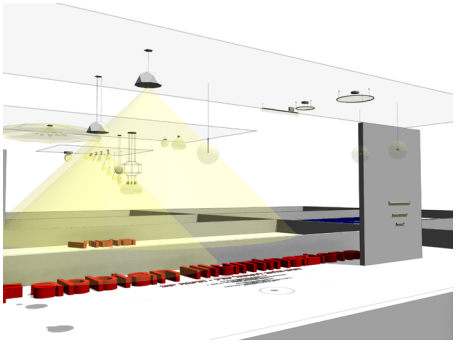

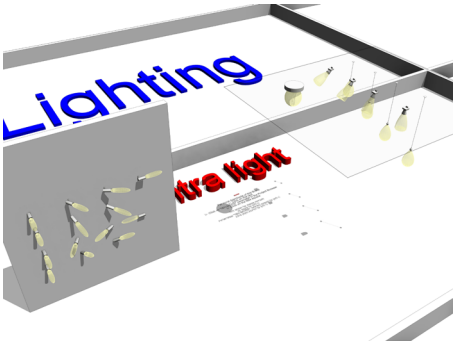

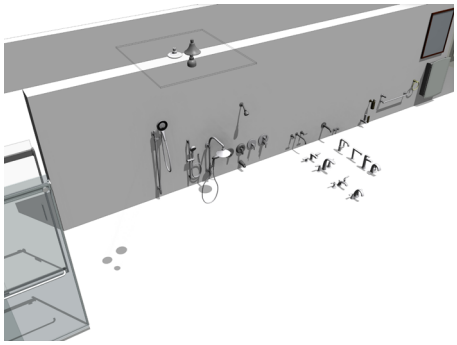

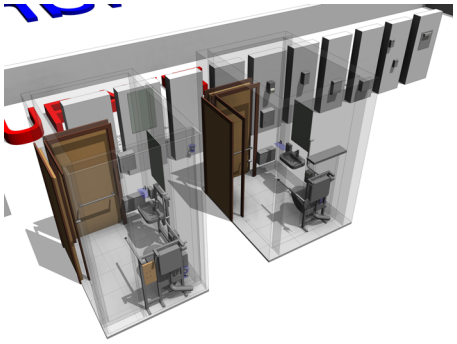


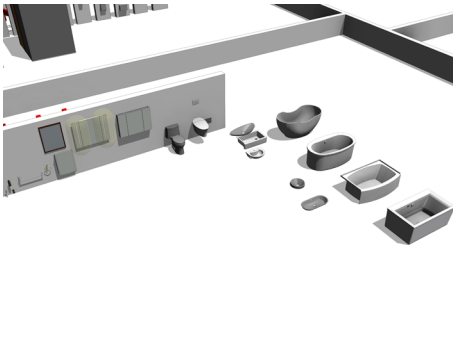



כל הזכויות שמורות לאלי שוקרי | איש אדריכלים בע"מ
www.ish.co.il | info@ish.co.il | 054-8811651
ISH simple to know


קטלוג ספריות AutoDesk

1. חלונות
2. דלתות
3. סניטריה
4. מכוניות
5. עצים
6. אביזרים למטבח
7. ועוד

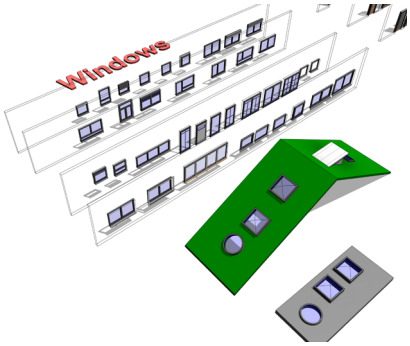


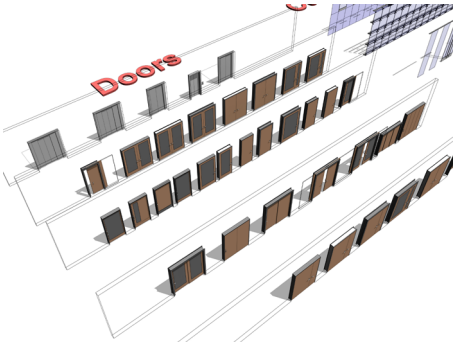


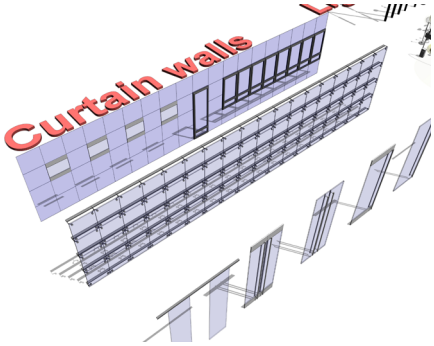


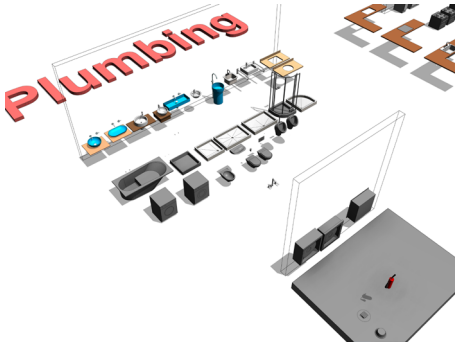




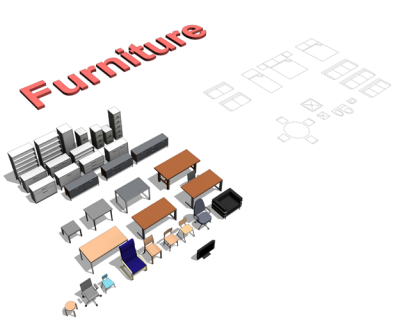


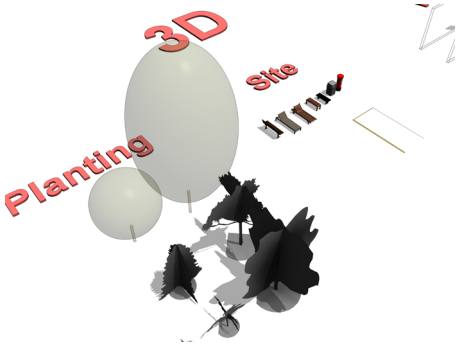


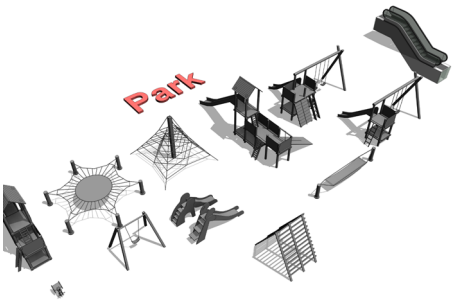



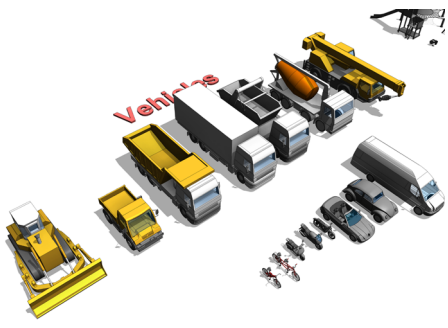

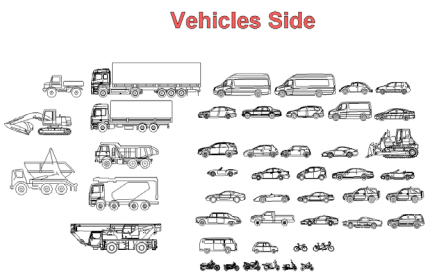

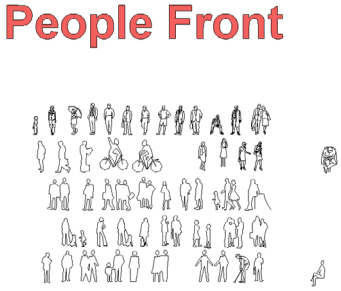


כל הזכויות שמורות לאלי שוקרי | איש אדריכלים בע"מ
www.ish.co.il | info@ish.co.il | 054-8811651
ISH simple to know


קטלוג ספריות AutoDesk

כל הDETAIL ITEMS לפרטים מהתקיה של אוטודסט פרוסים במקום אחד


1. פרופילים
2. ברגים
3. אטמים
4. ועוד

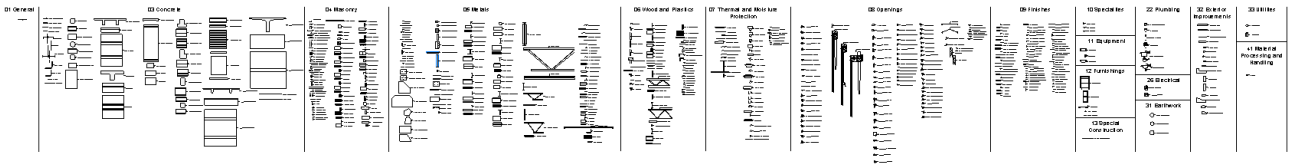


04 Masonry

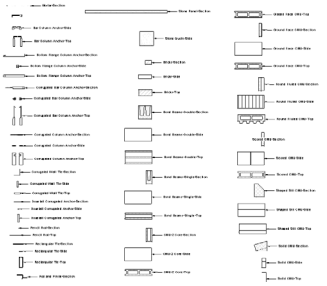


03 Concrete

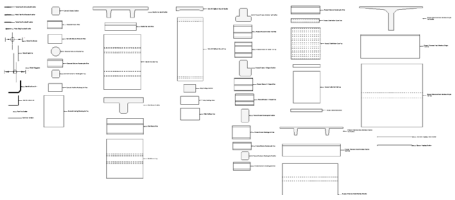


05 Metals

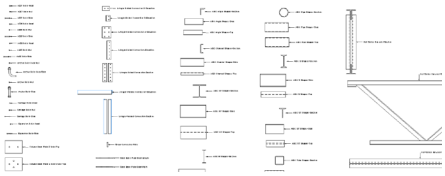

06 Wood and Plastics

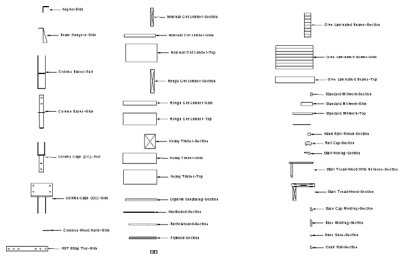


07 Thermal and Moisture Protection

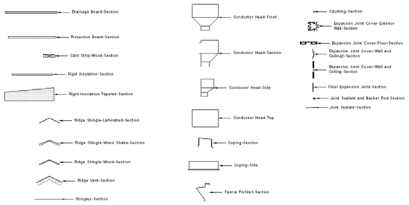

08 Openings



09 Finishes

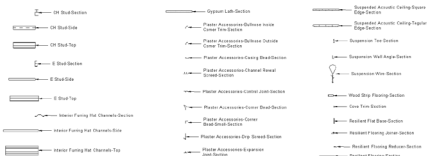


10 Specialties

11 Equipment

22 Plumbing

32 Exterior Improvements

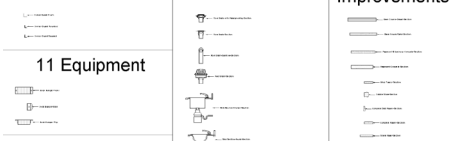

כל הזכויות שמורות לאלי שוקרי | איש אדריכלים בע"מ
www.ish.co.il | info@ish.co.il | 054-8811651
ISH simple to know

מוזמנים ליצור איתנו קשר לכל שאלה ועניין
לגבי הטמפלט וההכשרות שלנו

באתר www.ish.co.il
במייל info@ish.co.il
טלפון/וואטסאפ 054-8811651

אנחנו כאן לכל שאלה

בהצלחה

כל הזכויות שמורות לאלי שוקרי | איש אדריכלים בע"מ
www.ish.co.il | info@ish.co.il | 054-8811651