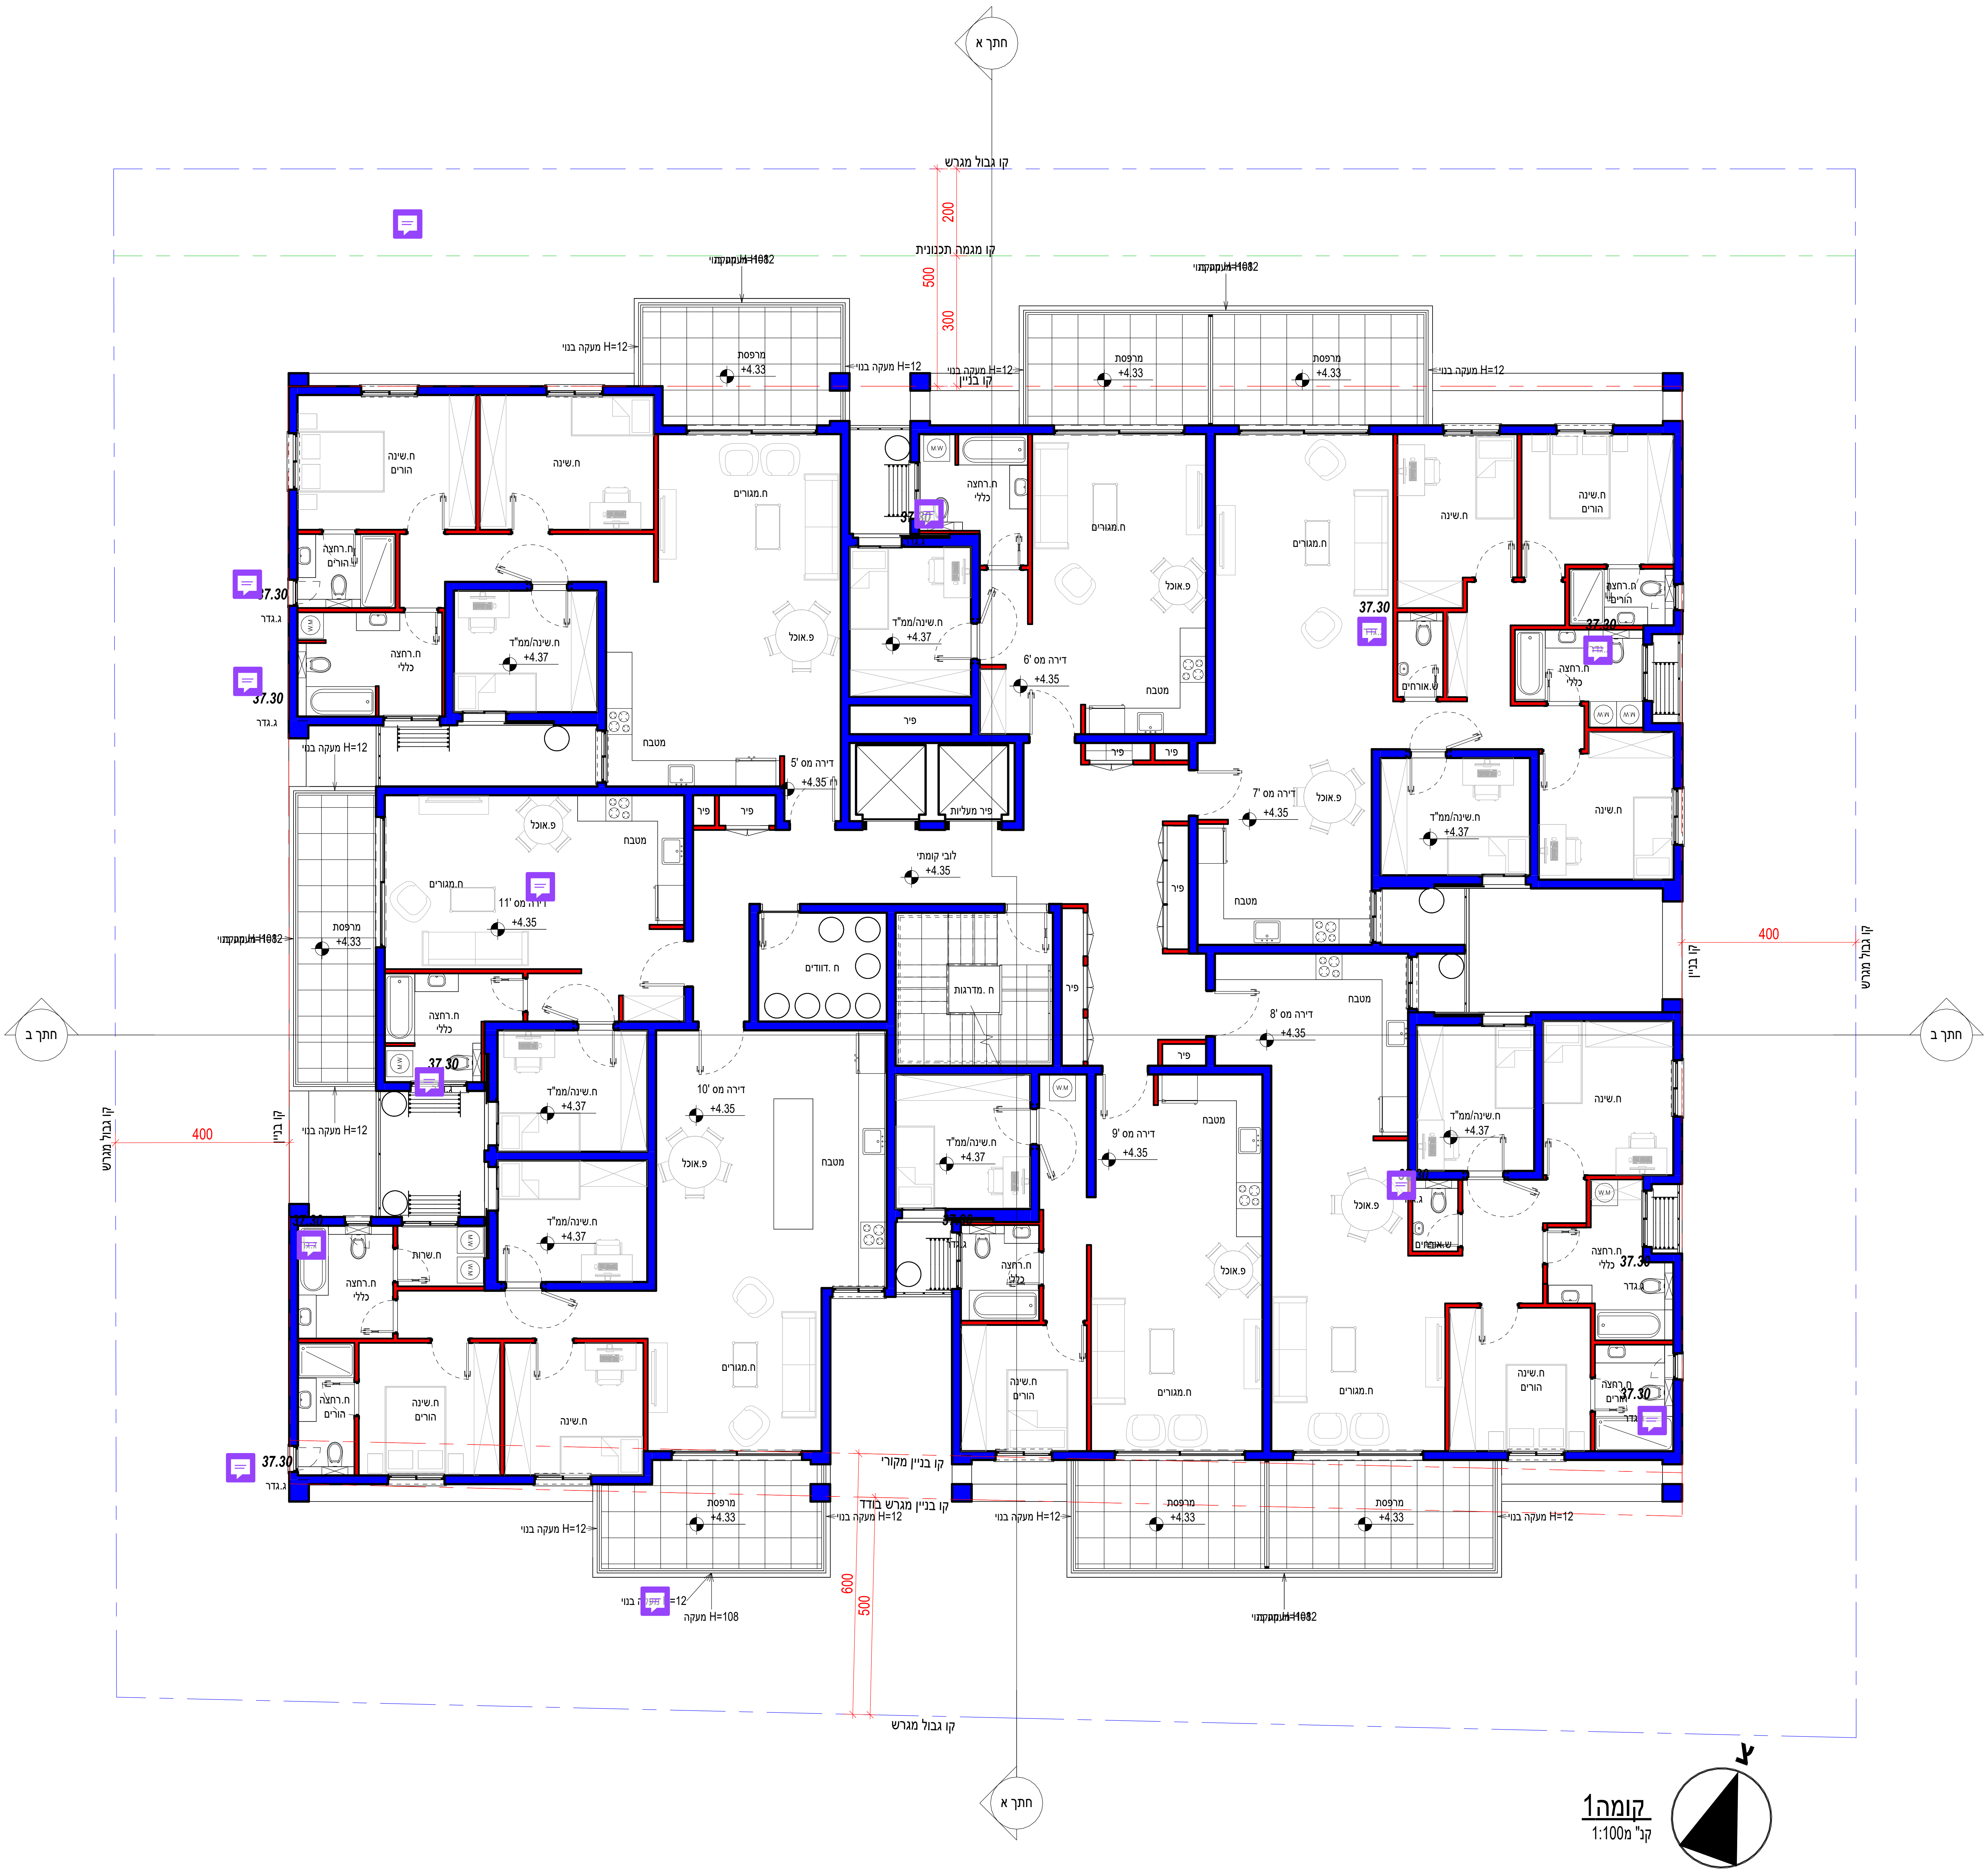
חתך א
קו גבול מגרש
קו מגמה תכנונית
200
500
300
מעקה H=108
מעקה בנוי H=12
מרפסת
+4.33
קו בניין
ח.שינה
הורים
ח.שינה
ח.מגורים
ח.רחצה
הורים
ח.רחצה
כללי
ח.שינה/ממ"ד
+4.37
פ.אוכל
מטבח
37.30
ג.גדר
דירה מס' 5
+4.35
דירה מס' 6
+4.35
דירה מס' 7
+4.35
דירה מס' 8
+4.35
דירה מס' 9
+4.35
דירה מס' 10
+4.35
דירה מס' 11
+4.35
פיר
פיר מעליות
לובי קומתי
+4.35
ח. דודים
ח. מדרגות
ח.שרות
ש.אורחים
W.M
400
קו בניין
קו גבול מגרש
חתך ב
קו בניין מקורי
קו בניין מגרש בודד
600
500
צ

קומה1

קנ"מ 1:100