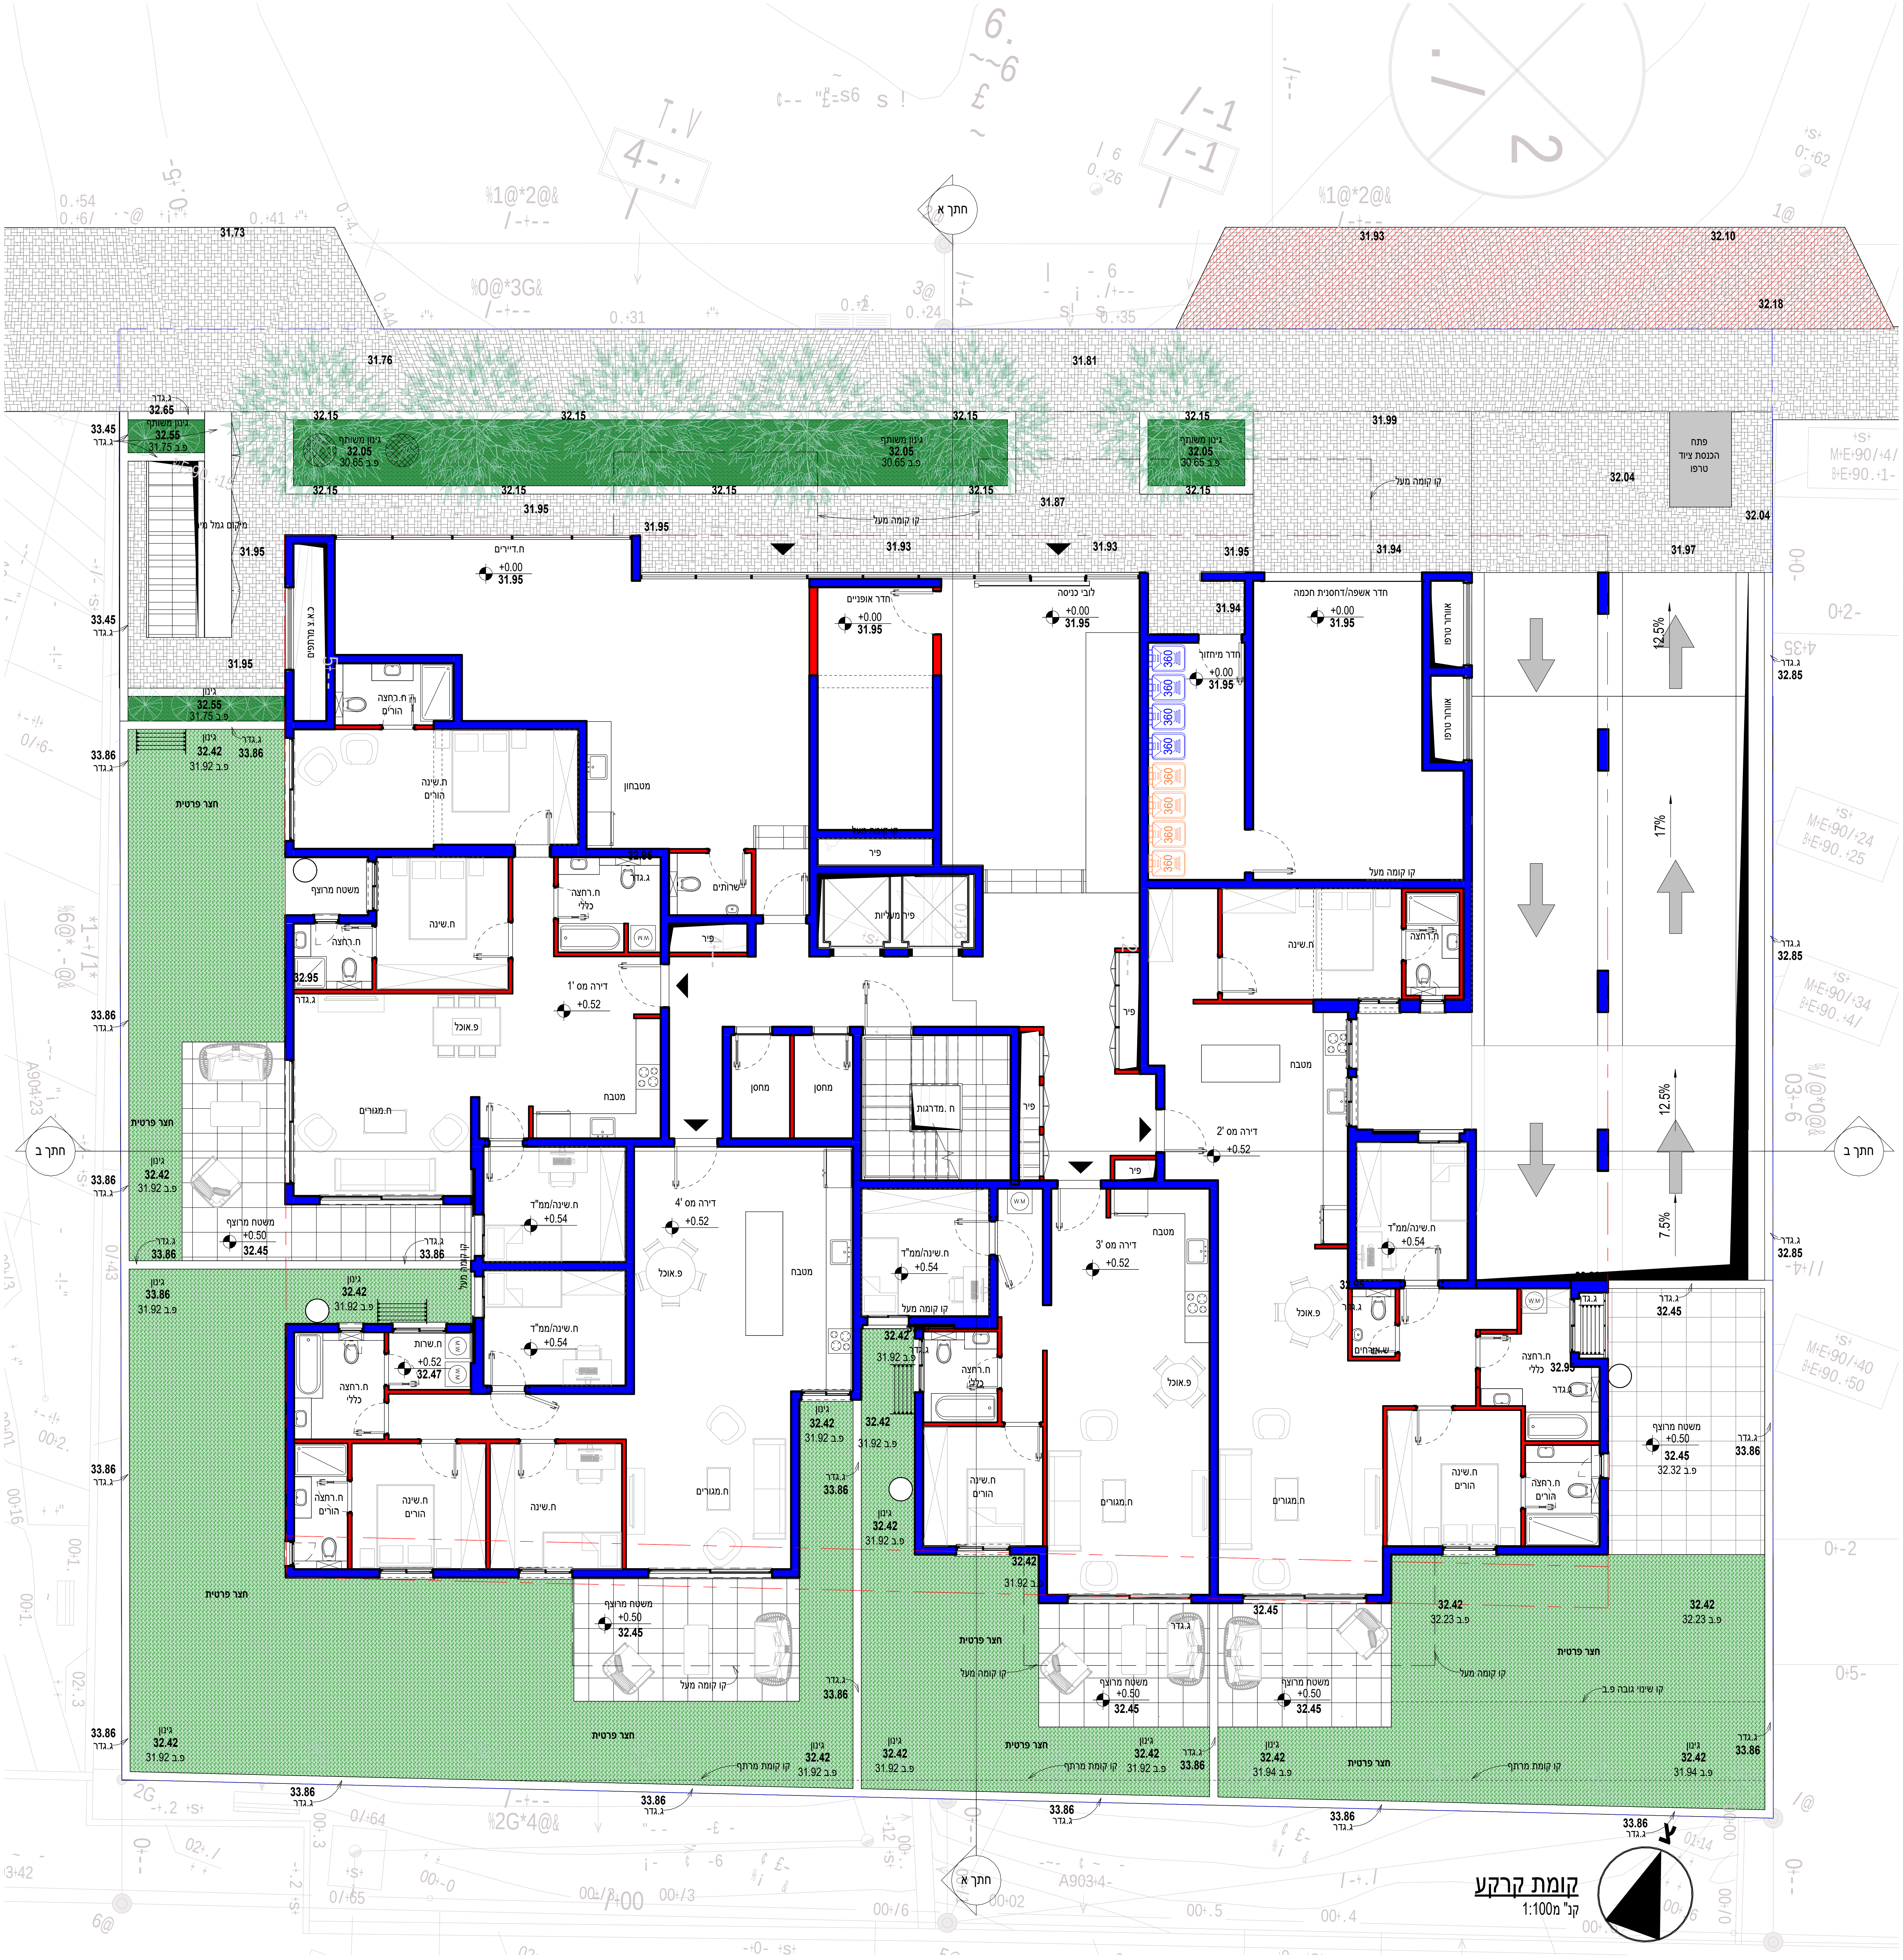
חתך א
חתך ב
ח.דיירים
+0.00
31.95
לובי כניסה
חדר אופניים
חדר מיחזור
חדר אשפה/דחסנית חכמה
אוורור טרפו
פתח הכנסת ציוד טרפו
גינון משותף
32.05
ב.ג 30.65
מקום גמל מים
ג.גדר
ג.א.ג מרופט
ח.רחצה הורים
ח.שינה הורים
מטבחון
שירותים
ח.רחצה כללי
ח.שינה
ח.רחצה
משטח מרוצף
+0.50
32.45
ג.גדר
33.86
דירה מס' 1
+0.52
פ.אוכל
ח.מגורים
מטבח
חצר פרטית
גינון
32.42
ב.ג 31.92
מחסן
ח. מדרגות
פיר
פיר מעליות
דירה מס' 2
דירה מס' 3
דירה מס' 4
ח.שינה/ממ"ד
+0.54
ח.שרות
+0.52
32.47
קו קומה מעל
קו קומה מרתף
קו שינוי גובה ג.ב
12.5%
17%
7.5%
31.73
31.76
31.81
31.93
32.10
32.18
32.41
32.15
31.99
32.04
31.87
31.95
31.94
31.97
33.45
32.65
32.55
ב.ג 31.75
32.85
32.23
31.94
32.32
32.95
W.M
360

קומת קרקע

קנ"מ 1:100