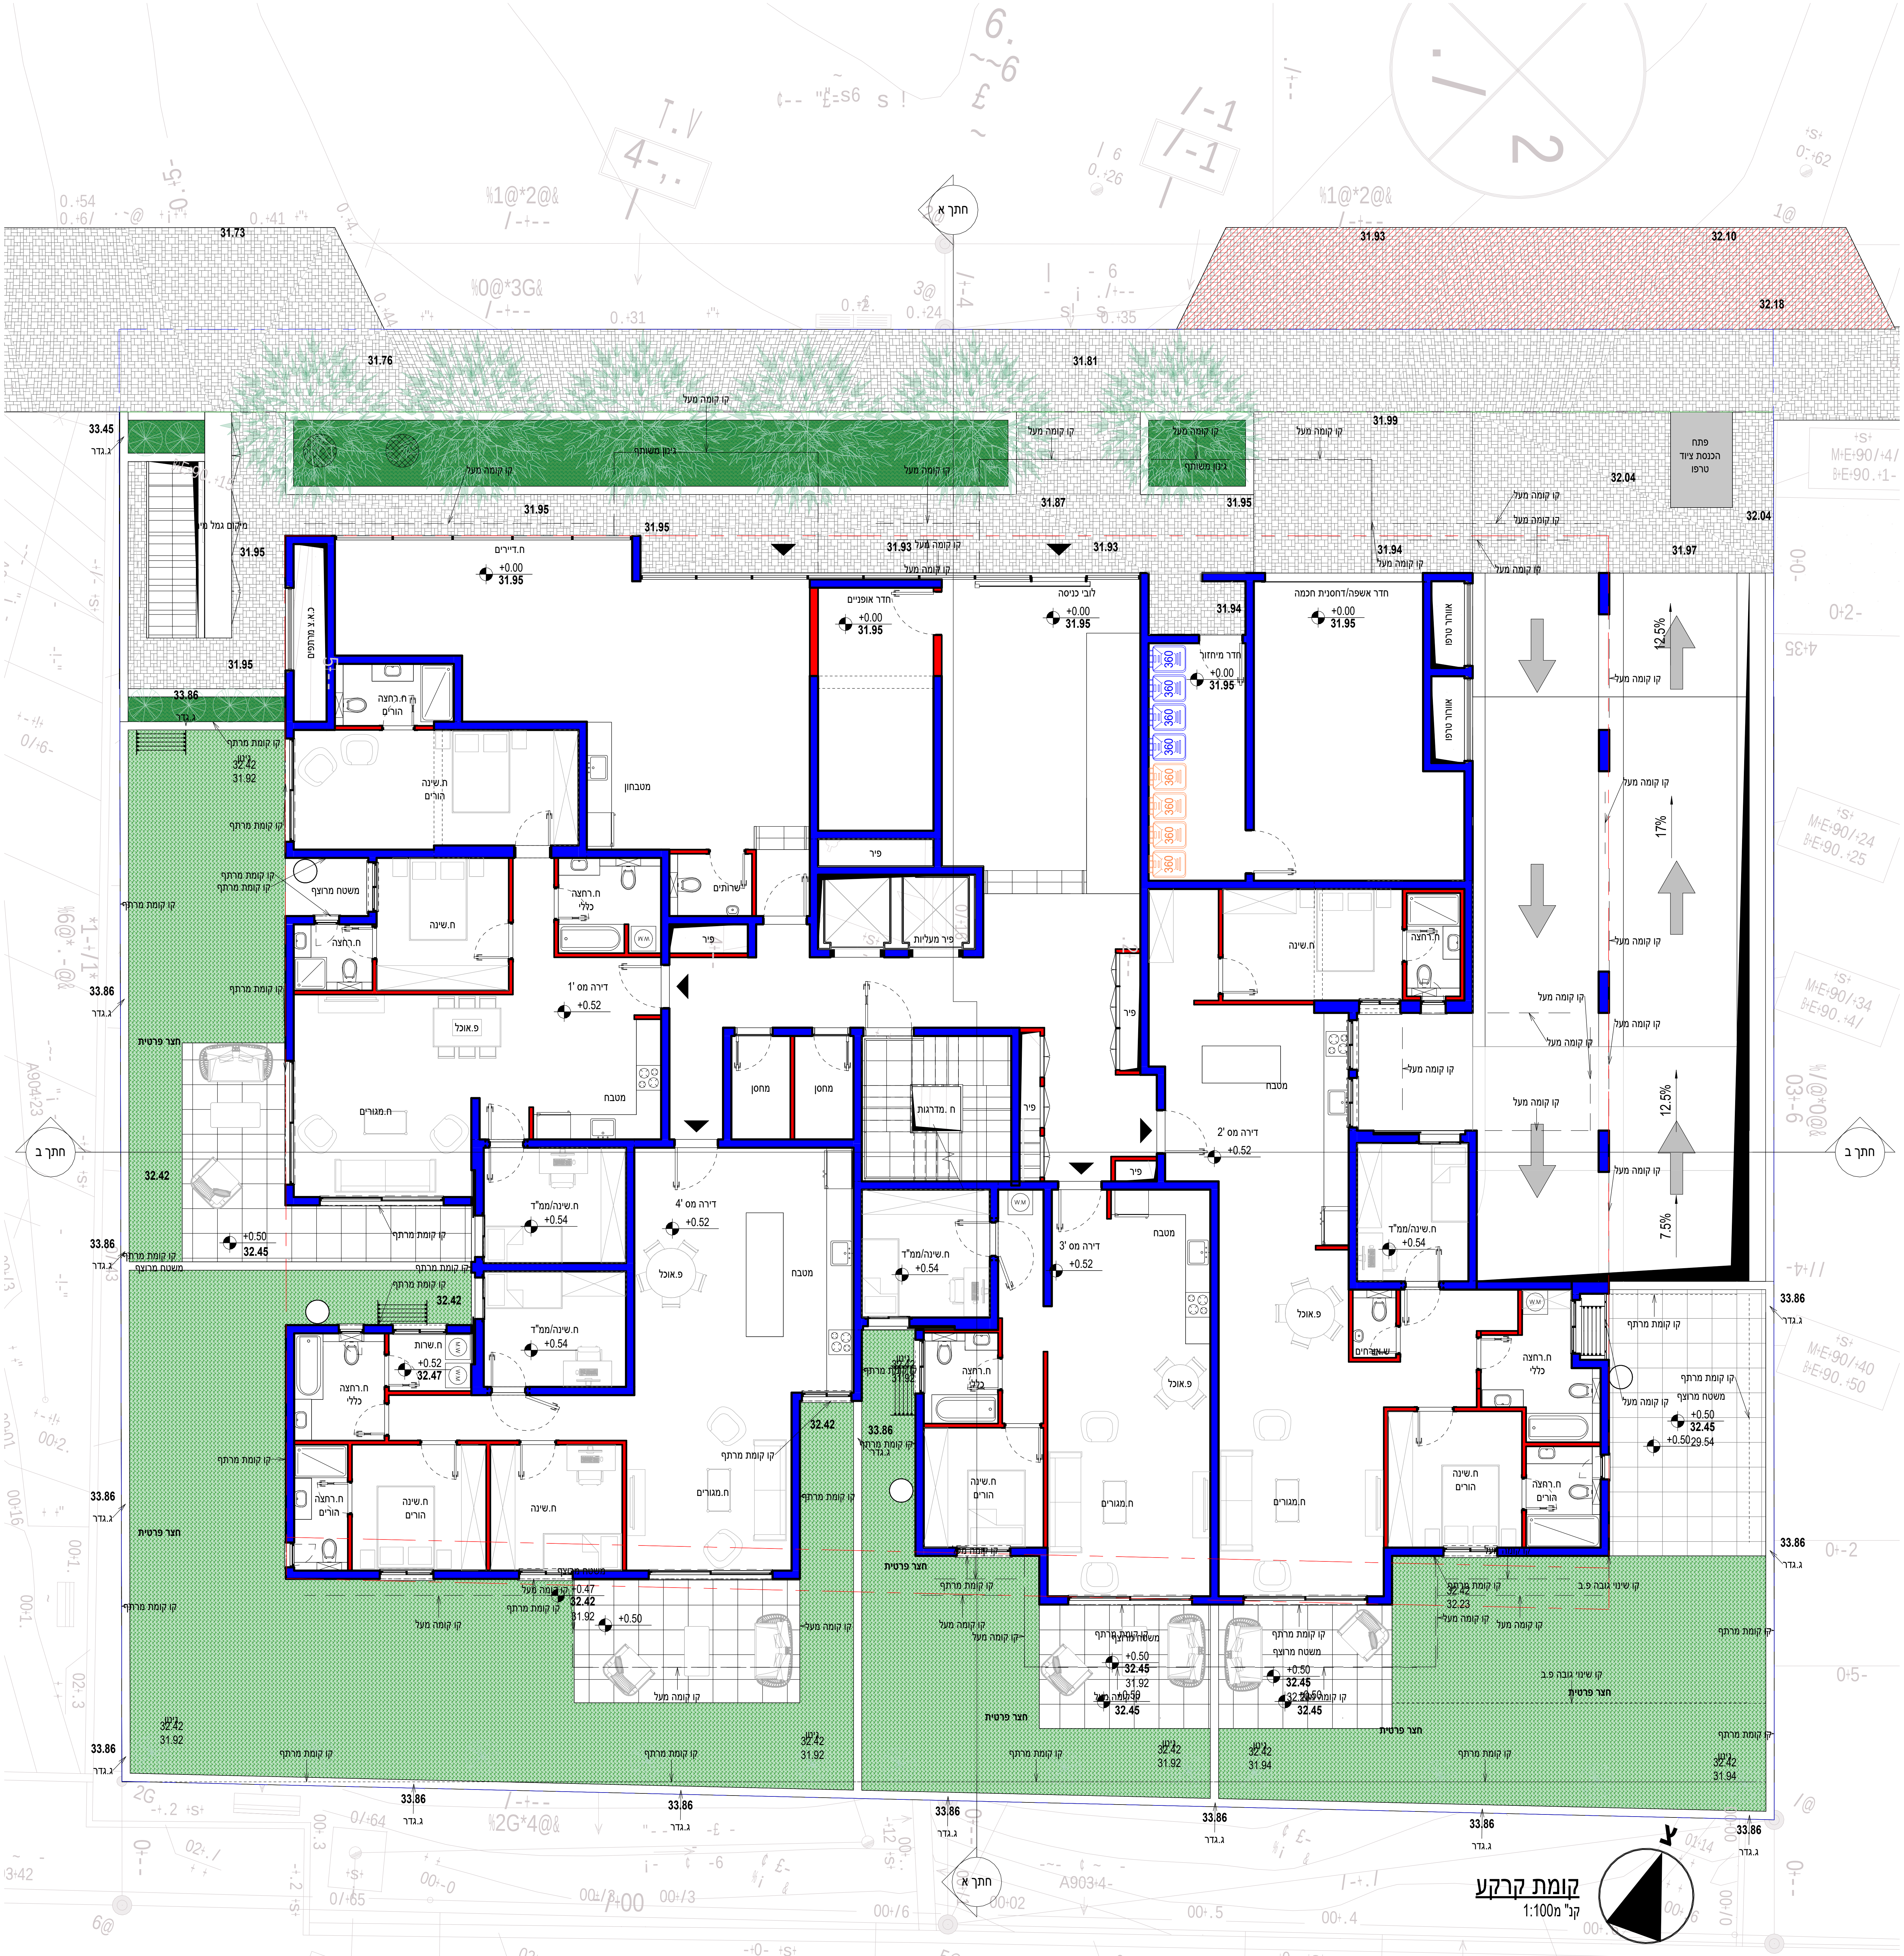
חתך א
חתך ב
צ
ח.דיירים
+0.00
31.95
חדר אופניים
לובי כניסה
חדר אשפה/דחסנית חכמה
חדר מיחזור
מיקום גמל מים
פתח הכנסת ציוד טרפו
גינון משותף
קו קומה מעל
קו קומת מרתף
דירה מס' 1
+0.52
דירה מס' 2
דירה מס' 3
דירה מס' 4
ח.שינה
ח.שינה הורים
ח.רחצה הורים
ח.רחצה כללי
ח.שינה/ממ"ד
ח.שרות
ח.מגורים
פ.אוכל
מטבח
מטבחון
שירותים
משטח מרוצף
מחסן
ח. מדרגות
פיר
פיר מעליות
חצר פרטית
ג.גדר
33.86
32.42
31.92
31.94
32.45
+0.50
+0.54
31.73
31.76
31.81
31.93
32.10
32.18
31.99
32.04
31.97
31.87
31.95
12.5%
17%
7.5%
360

קומת קרקע

קנ"מ 1:100